


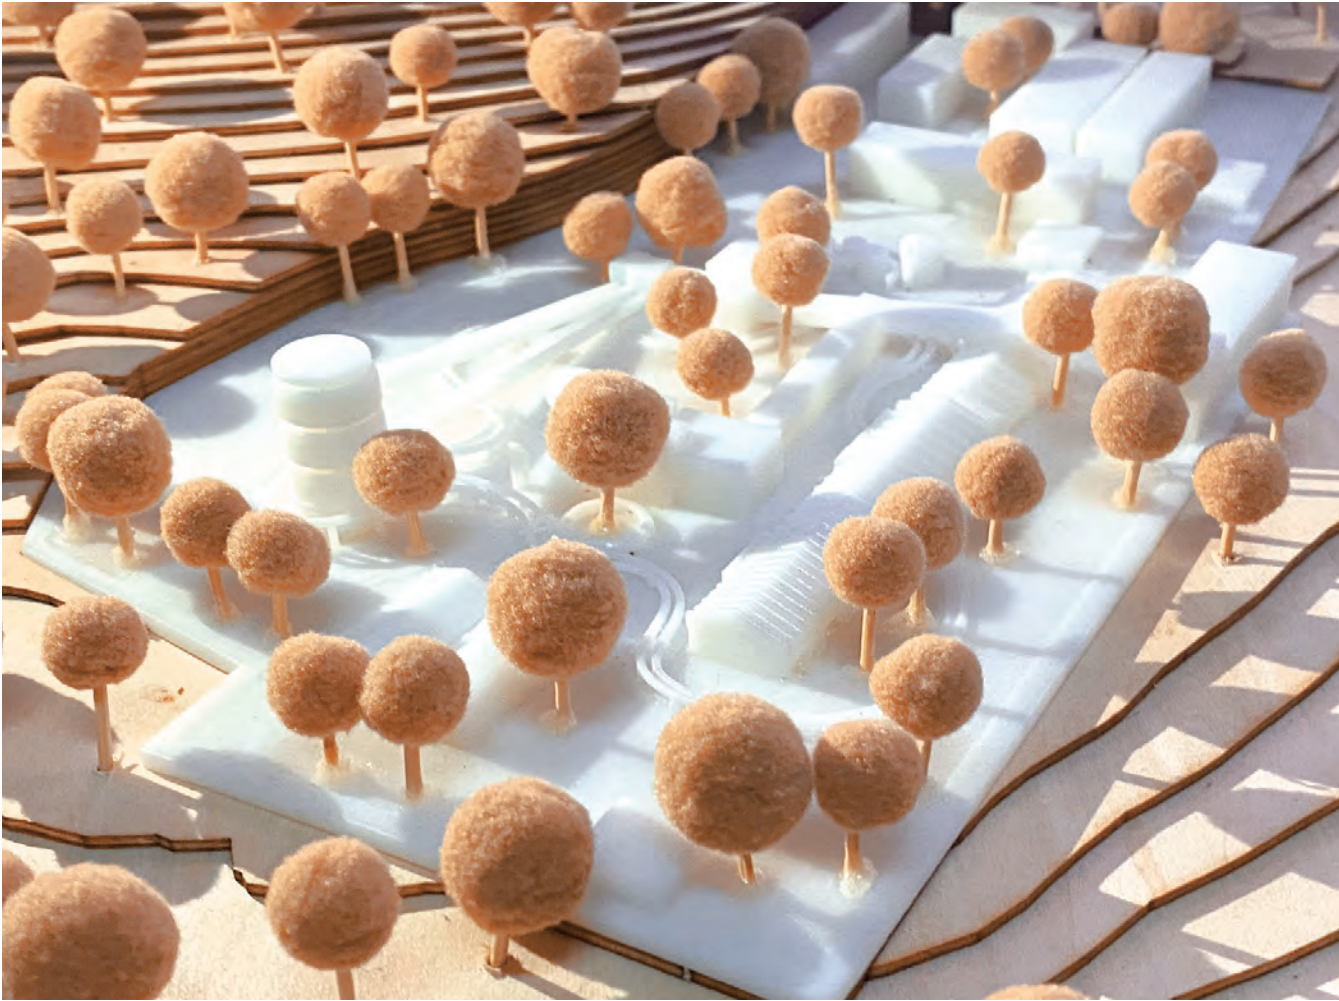

PARADISE ON RUINS


Wangping Coal Mine Resort Park Renovation Project

September 2023 to December 2023
Location: Wangping Village, Mentougou District, Beijing
Individual work in TianJin Renai University

With the development of modernism, landscape design has gradually penetrated into the transformation of land and society under the influence of the times, and has become an important part closely related to people today.

In the overall planning and design, in order to make people feel the significance of the coal mining industry under the changes of different eras, the traces of natural erosion of the site are retained in the design, and the industrial elements are transformed, reorganized and regenerated, making it a "lost joy" "An experiential space with a sense of "entertainment".

SITE ANALYSIS

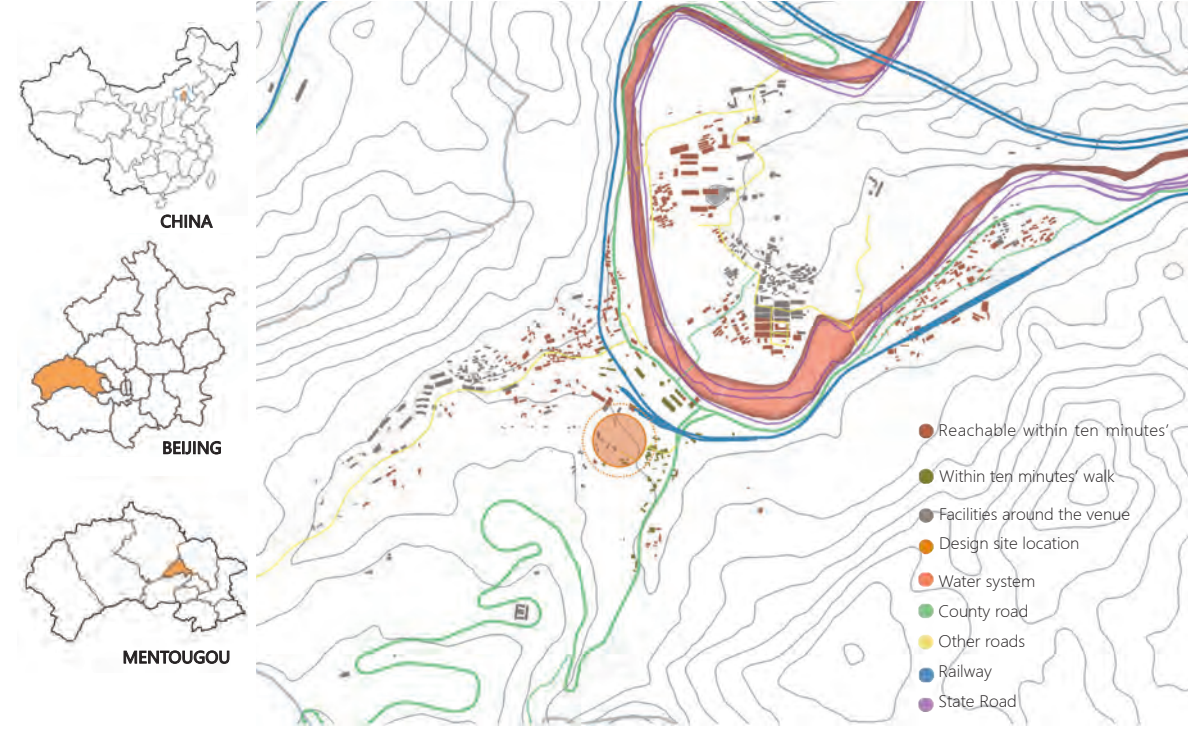

SITE HISTORY

1937 The Japanese army used force to mine coal mines
After the "Marco Bridge Incident" in 1937, the Japanese army invaded Beijing and destroyed the gate. Mentougou and Fangshan and other places were regarded as an important strategic material. They used force to open the Datou Coal Mine, the Mentougou Coal Mine under military control, and the forced occupation of Changgou Valley in Fangshan.

1960 Wangping village mining area named "Wangping Coal Mine"
In 1960, the Wangpingcun mining area was established independently and named: Wangpingcun Coal Mine. In March 1964, Wangpingcun Coal Mine merged with Anjiatan Coal Mine and was called Wangpingcun Coal Mine. It is sometimes referred to as "Wangpingcun Mine" or "Wang Mine" within the Mining Bureau.

1994 Wangping Coal Mine suspends production and guards
In 1994, due to the saturation of the coal market and the fact that the mine mostly produced low-calorie Carboniferous coal, the Ministry of Coal approved on October 26 that the Wangpingcun Coal Mine would cease production and be under supervision with immediate effect.

2016 Wangping Coal Mine officially blocks the wellhead
It took 22 years before the wellhead was officially sealed in August 2016, and the mining license was canceled in October of that year. The work of blocking the wellhead and canceling the mining license was organized and implemented by Beijing Haohua Energy Co., Ltd. (blocking the wellhead is an important indicator for checking whether the coal mine is closed).

SITE STATUS AND RENOVATION ISSUES SOLUTIONS

1. The industrial heritage is revitalized, the functions need to be updated, and the site lacks vitality.

2. Highlight the industrial properties of the site and transform them.

3. Properly update site functions to stimulate site vitality.

1. The site has been abandoned for too long and the building structure has been severely damaged.

2. Part of the building structure was retained and updated.


1. The lack of spiritual culture of the venue era.

2. Retain the unique cultural symbols of the site and transform them.

DESIGN STRATEGY


CULTURE

Cultural entertainment is entertainment where you can learn about the cultural knowledge of the mine through play.

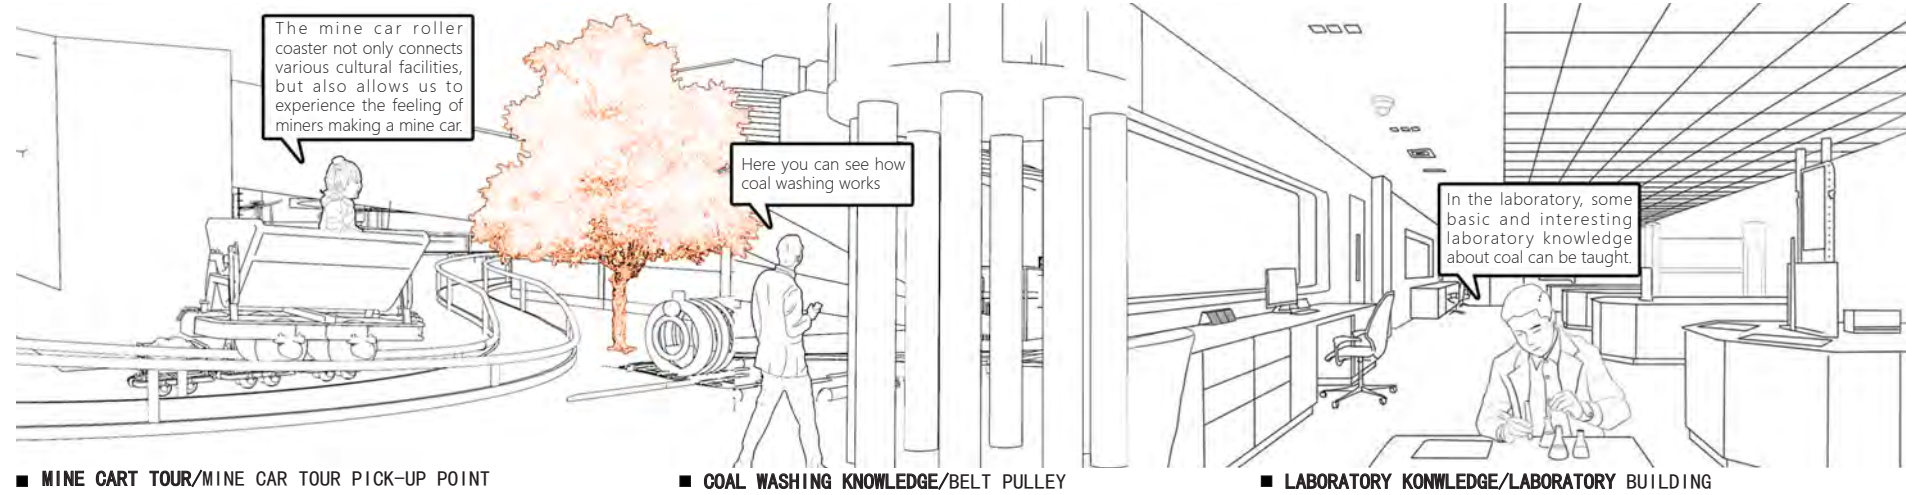


SPRIT

Spiritual entertainment is entertainment that allows people to feel the spirit of the times during play

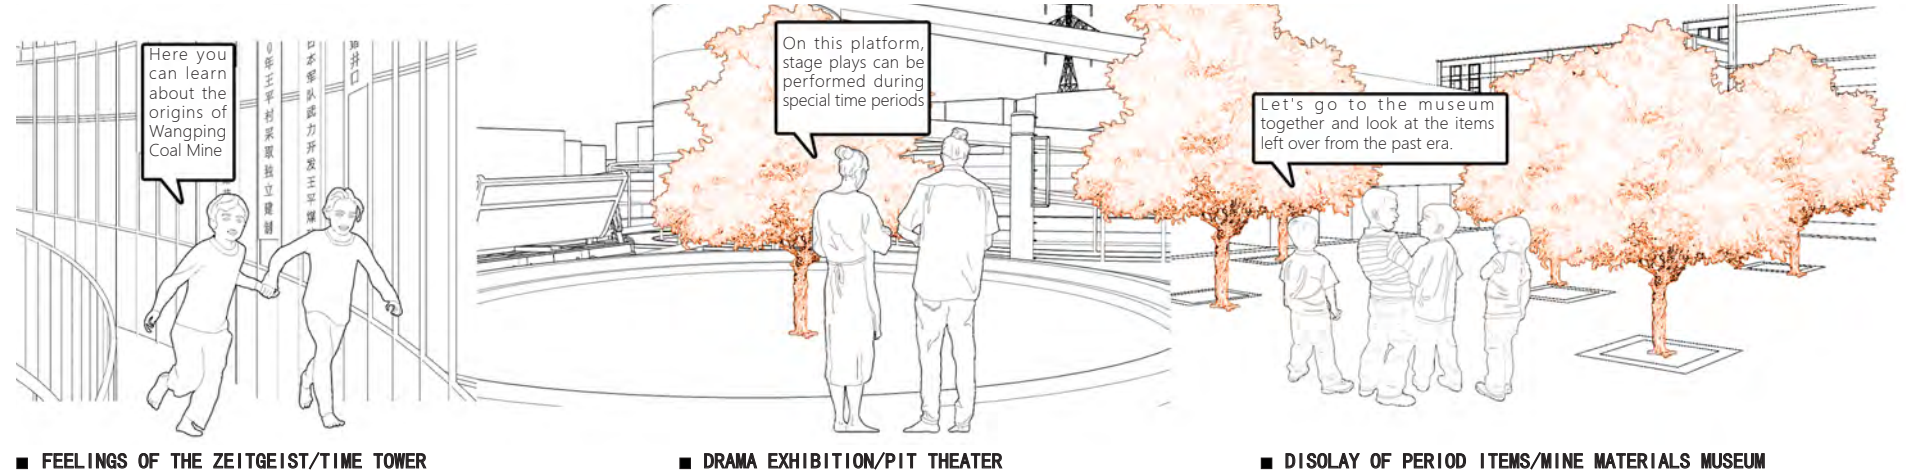

LIFESTYLE

Physical entertainment is entertainment that brings relaxation to the body

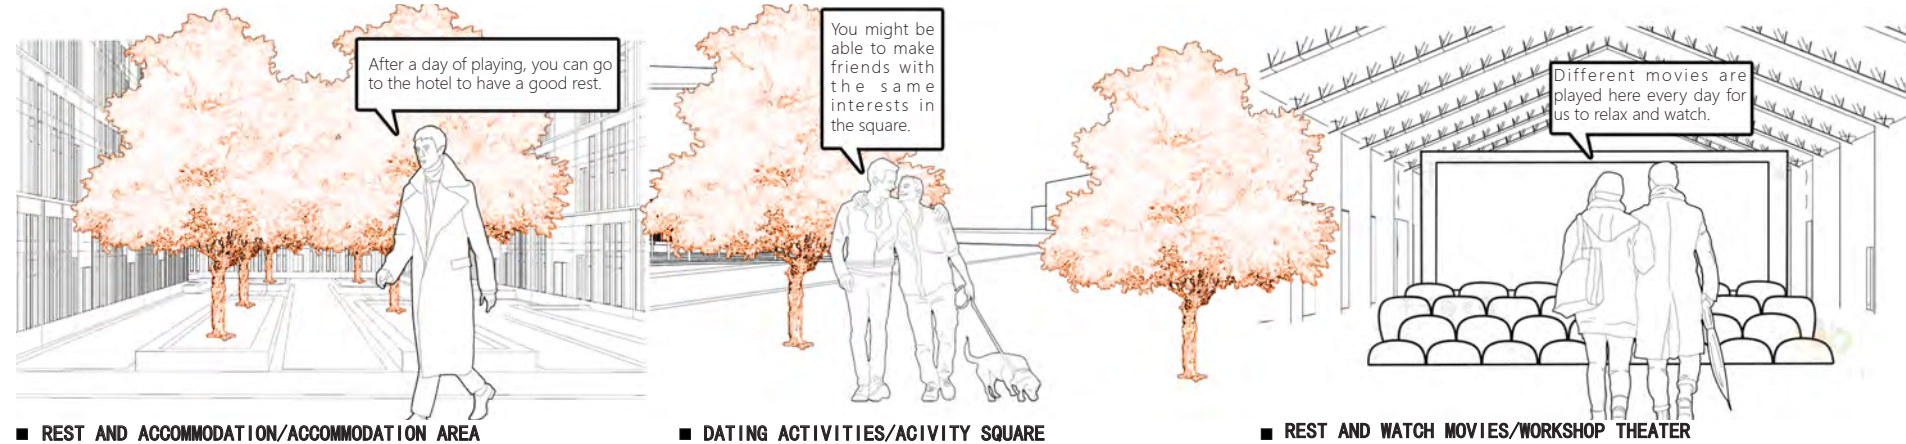

SITE MASTER PLAN



ACCOMMODATION

- 01.Homestay (Miners' quarters)
- 02.Boutique vhotel (Miners' quarters)
- 03.Youth hostel (Mining area office)
- 04.Accommodation area front desk (Equipment room)

LIFESTYLE

- 05.Parking lot (Abandoned vacant lot)
- 06.Restaurant (Workshop)
- 07.Workshop cinema (Workshop)

SERVICE

- 08.Reception/Service/Office (Miner's bathroom)
- 09.Service station A (Mining area communication room)
- 10.Service station B (Equipment room)
- 11.Service station C (Vehicle repair shop)

ENTERTAINMENT

- 12.Mine museum building A (Coal loading building)
- 13.Mining adventure (Mine entrance equipment)
- 14.Coal mine knowledge museum (Transport belt starting point loading)
- 15.Theme activity square (Coal drying yard)

- 16.Coal mine purification knowledge explanation (Belt pulley)
- 17.Mine museum building B (Coal washing building)
- 18.Gift shop/Climb to the top and watch (Coal storage tank)
- 19.Mine stage/Children's playground (Egradation pool)
- 20.Popularization of coal mine chemistry knowledge (Laboratory building)

0 5 10 20 50m



PROGRAMS


- Accommodation group
- Helper function group
- Park functional group
- Entertainment function group

CIRCULATION

- Play flow
- Traffic flow
- Accommodation flow

LANDSCAPE

- Parking lot
- Woods meadow
- Dense forest area
- Activity square
- Population square
- Accommodation flow

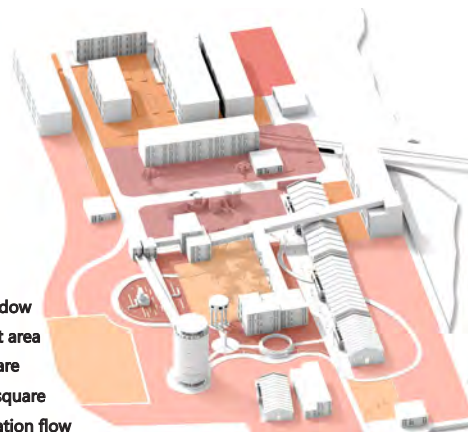

RENDERING OF THE SITE AFTER RENOVATION



■ AERIAL VIEW OF THE VENUE

The site structure is generally divided into accommodation area and entertainment area, which are divided by the entrance square. The entertainment area is connected to the whole park by the mine car track. People can reach any area of the entertainment area through the mine car. The auxiliary function area of the park is on the right side of the entertainment area, where you can rest and replenish supplies during the tour. The accommodation area serves those who want to continue playing at the venue at night or need a long rest. After a day of playing, the venue can provide accommodation services for tourists to rest.




■ MINE CAR TOUR STOP AND REST POINT



■ MINE CAR TOUR PICK-UP POINT




■ ENTRANCE COAL STORAGE TANK LANDSCAPE

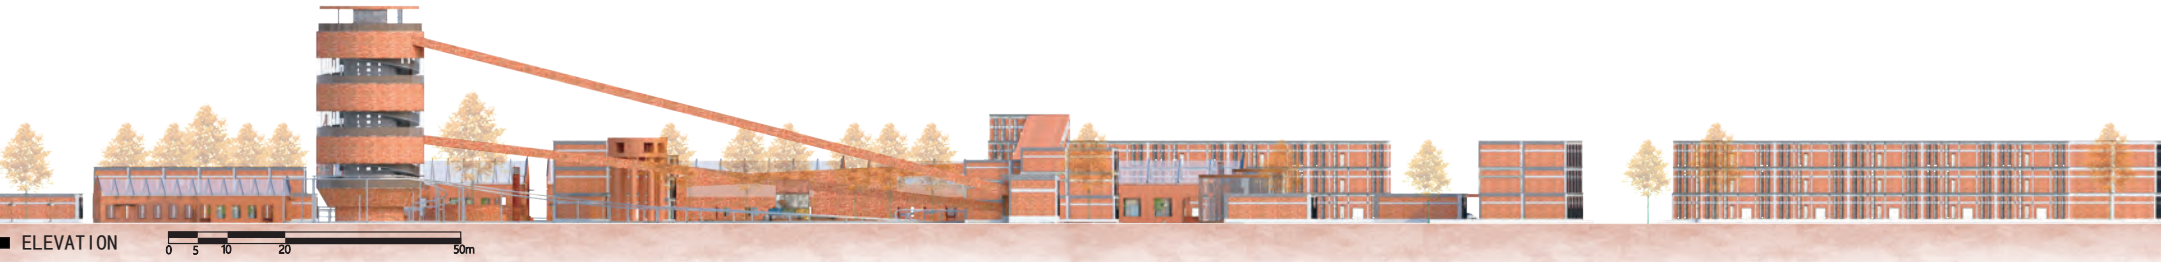


■ ELEVATION

TIME TOWER DESIGN

■ FLOOR PLAN

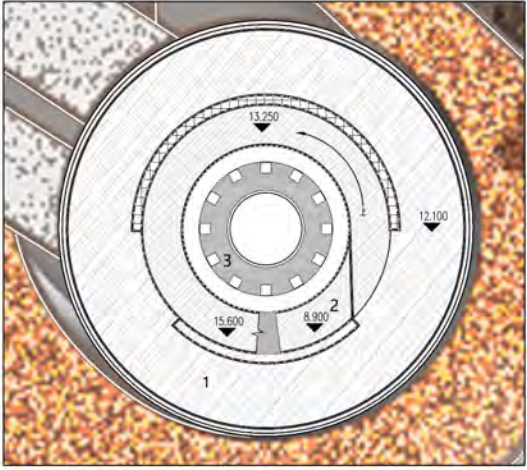

■ SECTION

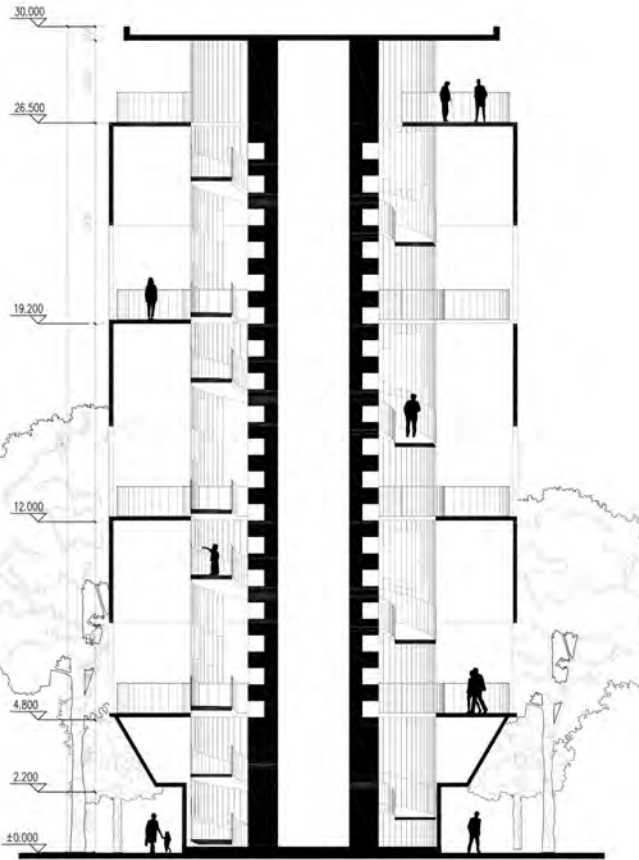

■ BUILDING FACADE TIMELINE



■ TIME RAMP



■ REST PLATFORM




■ MINE EXHIBITS DISPLAY



■ TIMES CULTURAL EXPERIENCE AREA



In the renovation design of the Time Tower in the key area, as people move towards the spiraling building tower, the objects related to the mine and the contemporary era will immerse them in the feelings of the culture of the times and the culture of the mine. As people continue to rise, they will slowly walk from the "past" to the "present". When people reach the top of the tower, they will see the entire transformed site. In the 30m ascending road, people can feel the charm of the changes of the times and the cultural spirit of the mine in the building.

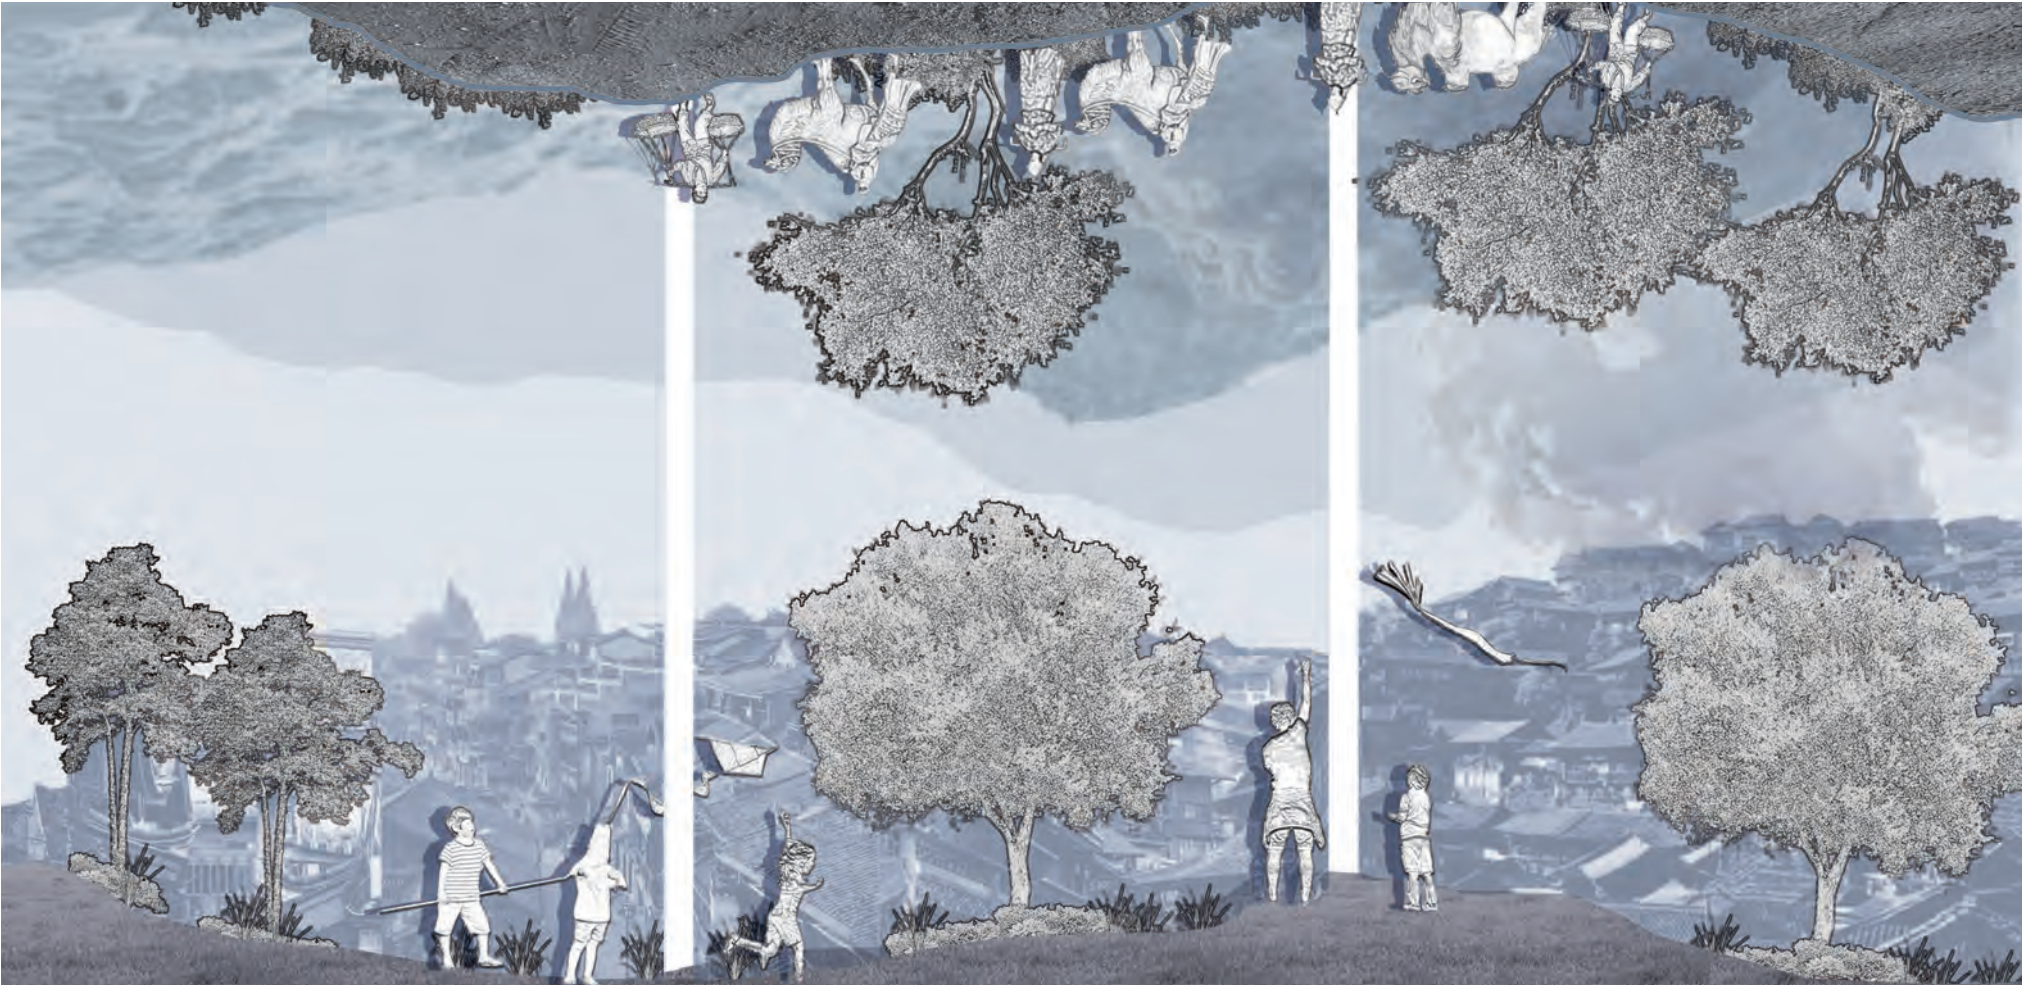

PROTECTION AND RENEWAL OF THE GRAND CANAL

Landscape construction project of Yangliuqing Ancient Town Park based on the concept of living inheritance

March 2023 to June 2023

Location: Yangliuqing Town, Xiqin District, Tianjin


Group work in TianJin University Renai College

Role in team: Exclusive design (including idea proposal, 3D modeling and analysis drawing)

Based on the connection between metropolitan space and technology, we believe that people can create an "invisible city" where communication, interaction, and self actualization are constantly strengthening. In the "Landscape Construction Design of Yangliuqing Yuhe Park" project, in order to explore the experiential expression of local culture and canal culture in Yangliuqing with distinctive features, and to cooperate with the government to create a landmark intangible cultural heritage experience IP.

By refining the different cultural characteristics of each dynasty, four dynasty galleries were created on the south bank of the canal to promote the canal culture. On the north bank of the canal, a Yangliuqing cultural experience venue is created based on the local cultural line of Yangliuqing.

SITE ANALYSIS

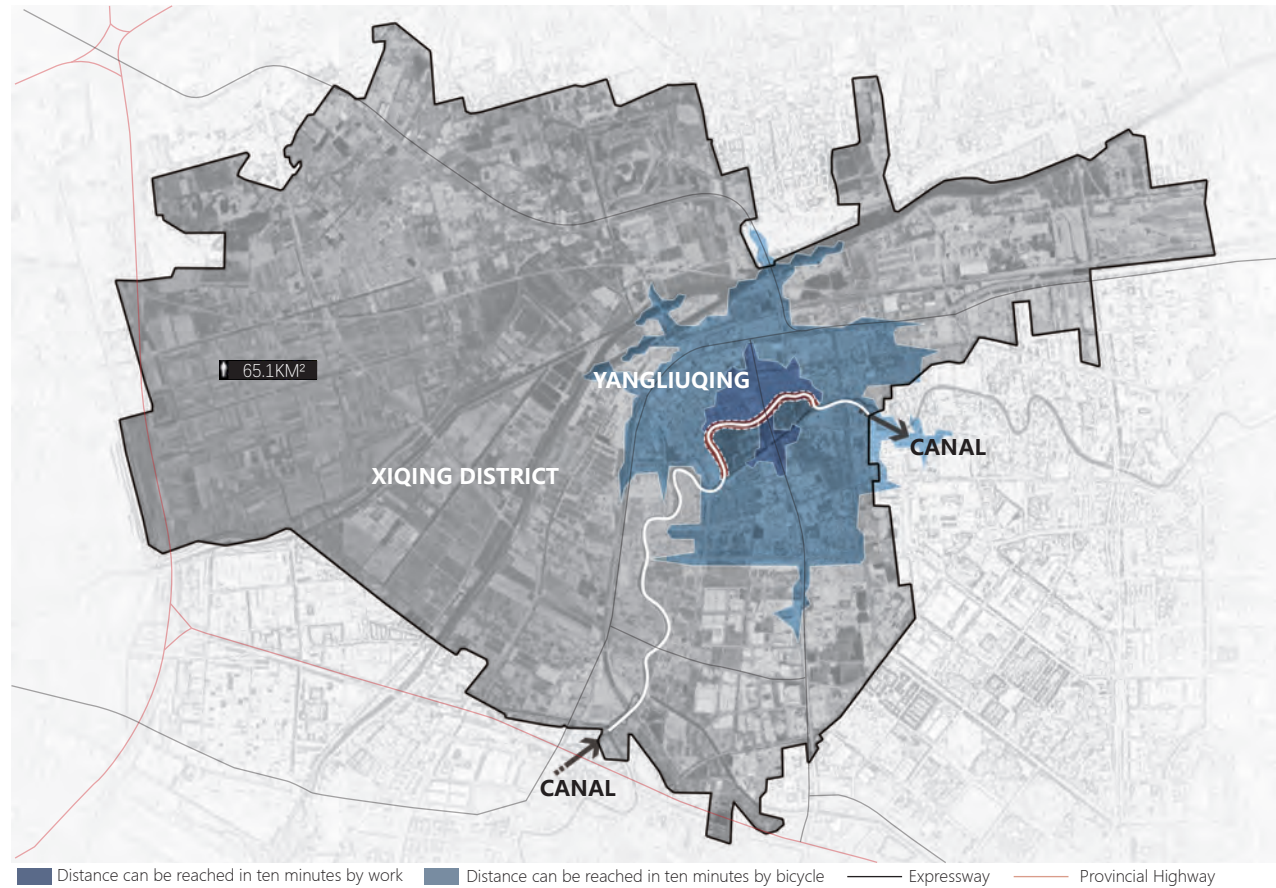


SITE POI POINT OF INTEREST

• Famous tourist sites




• Catering Services

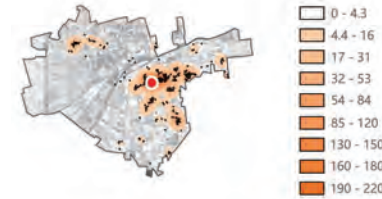

• Popular science and cultural services




• Domestic services

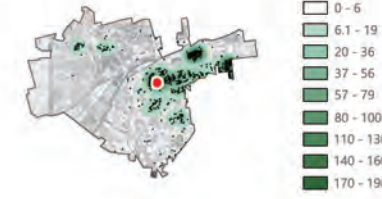


• Public Utilities




• Shopping service

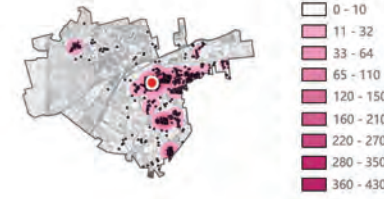

PROBLEM AND SOLUTION

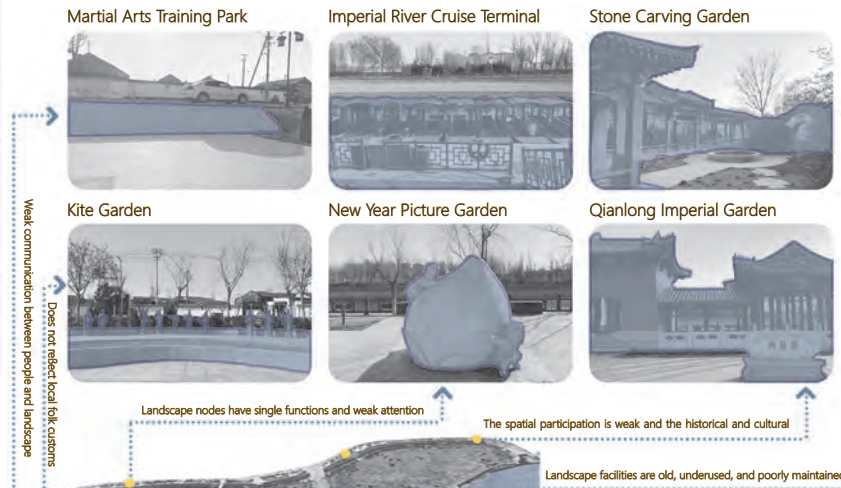

1. The ecology within the site also lacks
2. The damage to the natural environment is mainly manifested in water pollution .
3. Many facilities and roads in the park are in disrepair and have suffered extensive damage.
4. The design of the facilities did not take special groups into consideration.
5. The value of the canal has not been fully explored.
6. The expression of Yangliuqing culture and canal culture in the park is not perfect

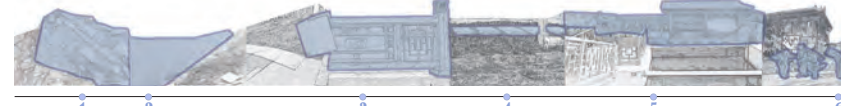

DESIGN STRATEGY

■ CIRCULATION DESIGN



■ PROGRAM DESIGN



■ LANDSCAPE DESIGN




- main road
- service road
- First level entrance guidance
- Secondary entrance guidance
- Cultural inheritance
- recreation
- Popular science education
- Sightseeing browsing
- Sports and fitness
- Main node
- Secondary node
- Landscape sight
- Landscape line

■ CULTURE SPOTS DESIGN

- 01.Light and shadow Gallery
- 02.Qing Dynasty Gallery
- 03.New Year Picture Gallery
- 04.Ming Dynasty Gallery
- 05.Stone Carving Gallery
- 06.Yuan Dynasty Gallery
- 07.Poetry monument
- 08.Song Dynasty Gallery



HISTORY TIMELINE

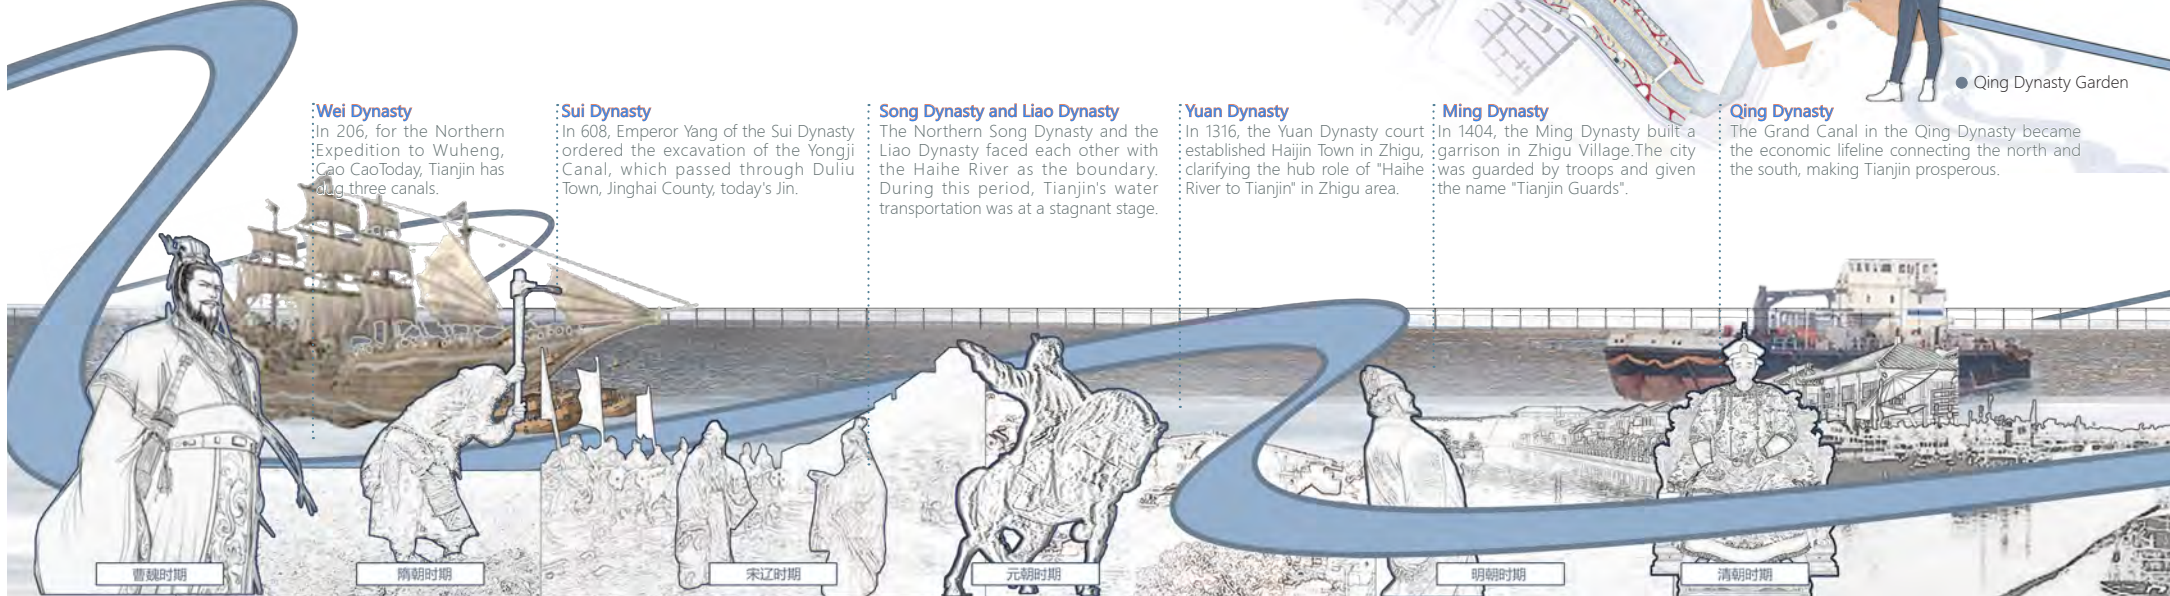

Wei Dynasty

In 206, for the Northern Expedition to Wuheng, Cao CaoToday, Tianjin has dug three canals.

Sui Dynasty

In 608, Emperor Yang of the Sui Dynasty ordered the excavation of the Yongji Canal, which passed through Duliu Town, Jinghai County, today's Jin.

Song Dynasty and Liao Dynasty

The Northern Song Dynasty and the Liao Dynasty faced each other with the Haihe River as the boundary. During this period, Tianjin's water transportation was at a stagnant stage.

Yuan Dynasty

In 1316, the Yuan Dynasty court established Haijin Town in Zhigu, clarifying the hub role of "Haihe River to Tianjin" in Zhigu area.


Ming Dynasty

In 1404, the Ming Dynasty built a garrison in Zhigu Village.The city was guarded by troops and given the name "Tianjin Guards".

Qing Dynasty

The Grand Canal in the Qing Dynasty became the economic lifeline connecting the north and the south, making Tianjin prosperous.

MASTER PLAN

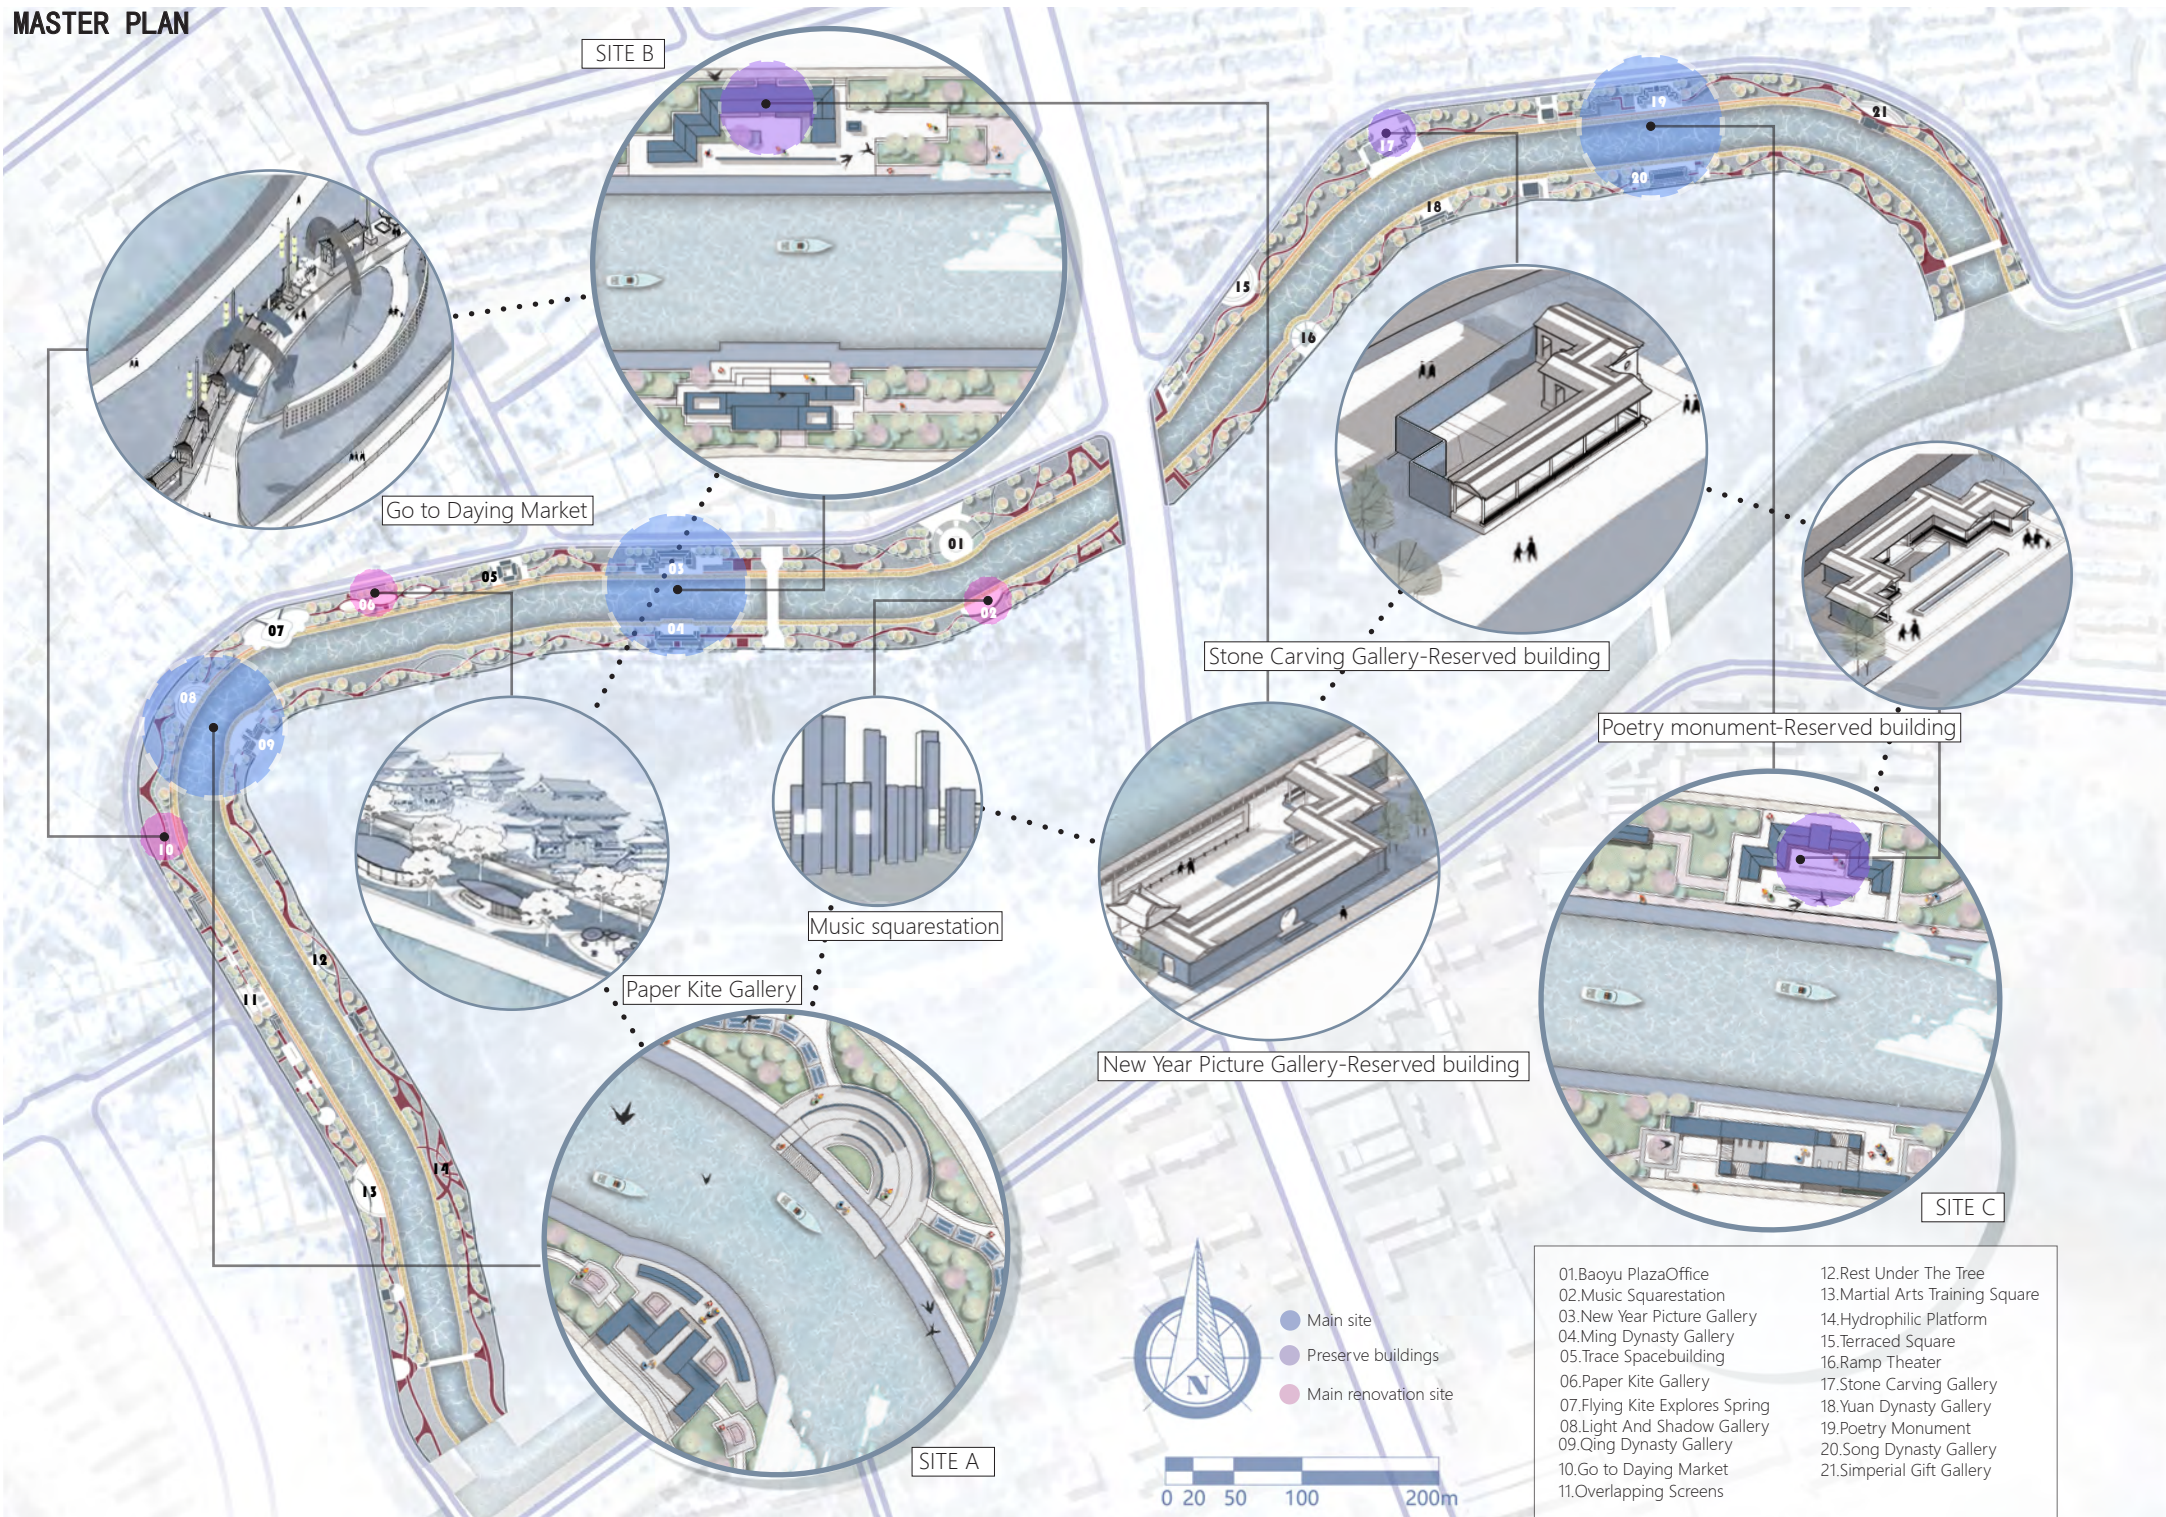

SITE B

Go to Daying Market

Stone Carving Gallery-Reserved building

Poetry monument-Reserved building

Music squarestation

Paper Kite Gallery

New Year Picture Gallery-Reserved building

SITE A

SITE C



0 20 50 100 200m


- 01.Baoyu PlazaOffice
- 02.Music Squarestation
- 03.New Year Picture Gallery
- 04.Ming Dynasty Gallery
- 05.Trace Spacebuilding
- 06.Paper Kite Gallery
- 07.Flying Kite Explores Spring
- 08.Light And Shadow Gallery
- 09.Qing Dynasty Gallery
- 10.Go to Daying Market
- 11.Overlapping Screens
- 12.Rest Under The Tree
- 13.Martial Arts Training Square
- 14.Hydrophilic Platform
- 15.Terraced Square
- 16.Ramp Theater
- 17.Stone Carving Gallery
- 18.Yuan Dynasty Gallery
- 19.Poetry Monument
- 20.Song Dynasty Gallery
- 21.Simperial Gift Gallery

NODE DETAIL DESIGN


■ SITE A




■ ELEVATION

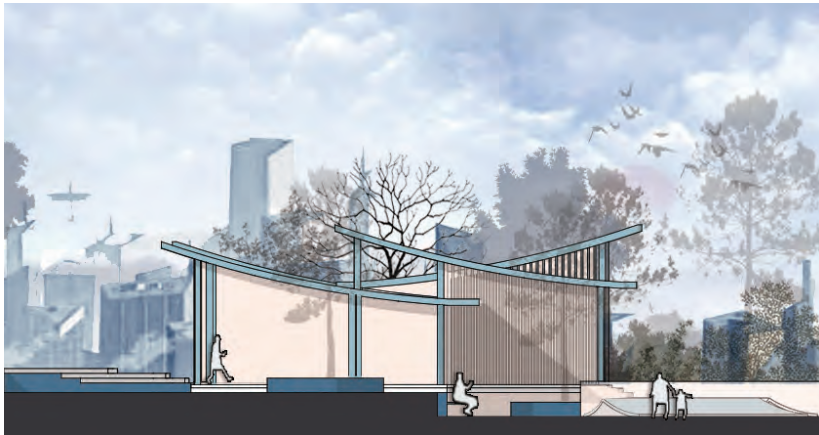


■ PLAN A

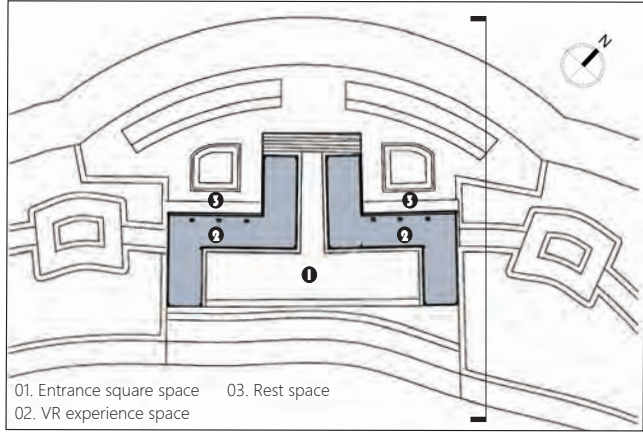


■ SITE B

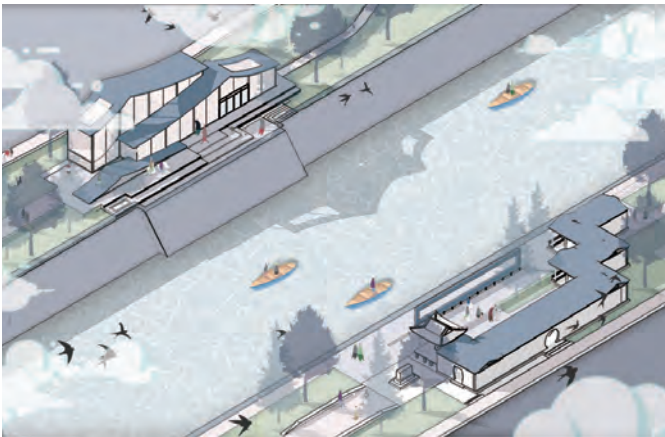


■ ELEVATION

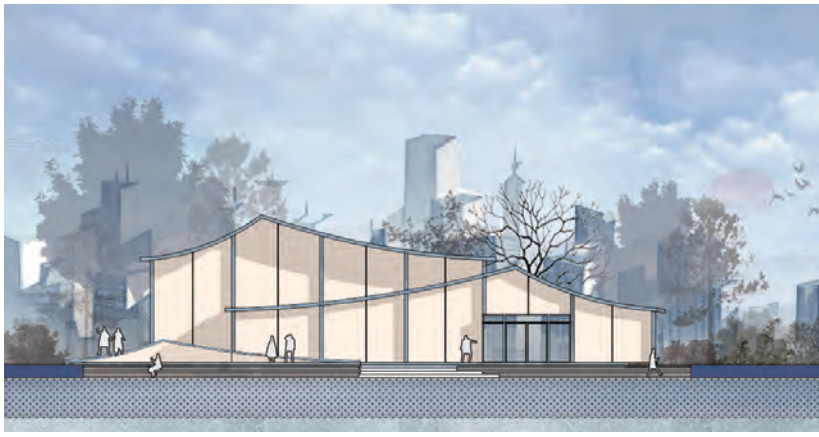


■ PLAN B

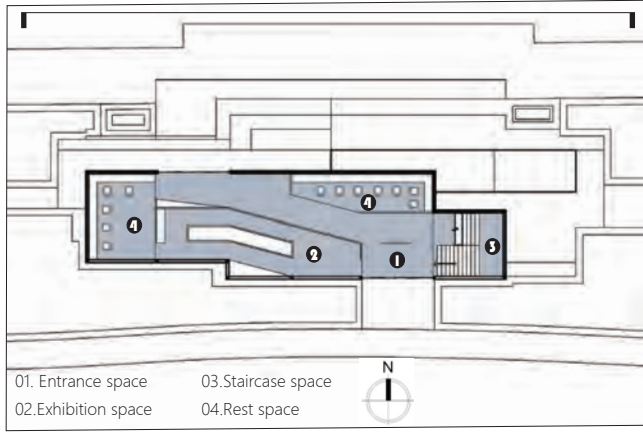


■ SITE C

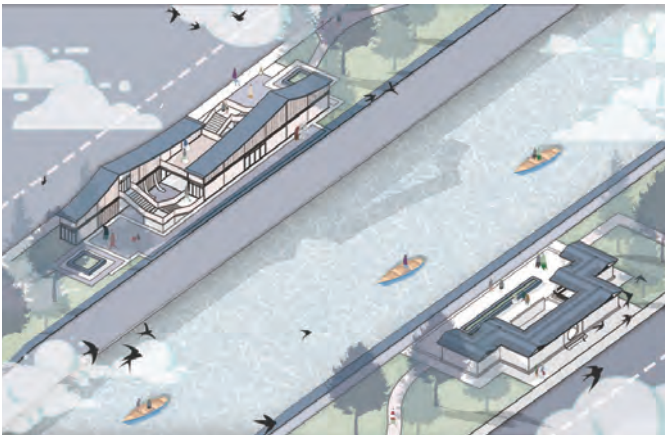

■ ELEVATION

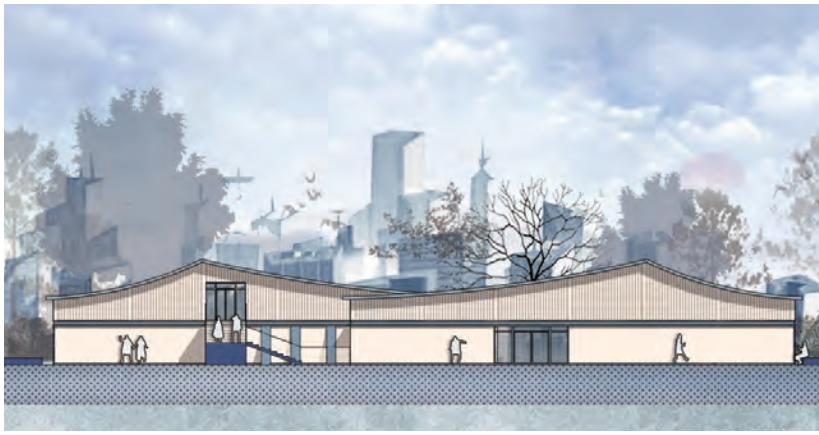

■ PLAN C

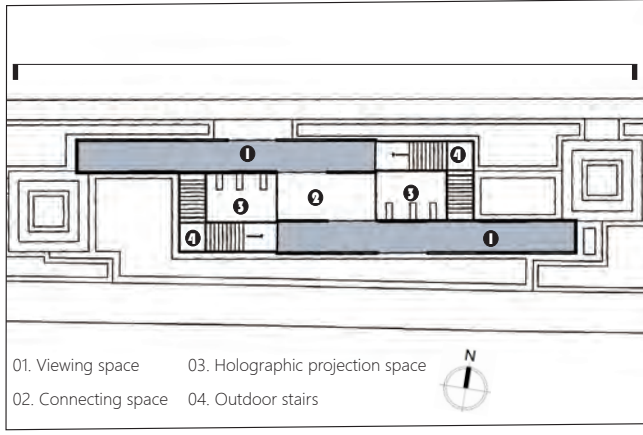

THE YANGLIUQING CULTURAL LINE ON THE NORTH BANK OF THE CANAL



The poetry monument records the poems of poets from ancient times to the present describing Yangliuqing. People can understand the meaning behind each ancient poem there. People can discuss poems here and dream back to the Song Dynasty.



In the New Year Painting Garden, people can not only watch the sea theater across the river, but also find hidden New Year painting dolls through unique symbols in the garden and listen to them tell the stories behind the New Year paintings.



On the Light and Shadow Corridor, the original square has been preserved and a seaside pier has been added, where people can experience boating and wandering in the canal for a better waterfront experience.



The Gandaying Cultural and Creative Market recreates the prosperous scene of Yangliuqing Gandaying in the venue. Tourists can experience the culture of Gandaying and purchase their favorite cultural and creative products in the market.



THE CULTURAL LINE OF DYNASTIES ON THE SOUTH BANK OF THE CANAL



In the Song Dynasty Garden, holographic projection technology is used to show visitors in the middle area of the building the story of the people who lost the war in the Song Dynasty and moved their families to Yangliuqing, giving people a more realistic perception.



The circular projection allows tourists to immerse themselves in the excavation period of the Yangliuqing section of the Grand Canal, and the interaction between the smart screen and tourists also increases the fun of the venue.



Between the Ming Dynasty garden and the New Year painting garden, a dreamlike sea theater was created for tourists using water curtain projection. People can sit on the staircase theater in front of the Ming Dynasty Garden to watch.



VR virtual reality technology is used in the Qing Dynasty Garden, allowing people to have conversations with the ancients in virtual reality and learn about their past and present lives and the development of Yangliuqing culture.





NEWBORN

Tree Burial Park Design in the Post-Industrial Era

September 2022 to December 2022

Location: Donzhuang Town, Xiuyu District, Fujian

Individual work in TianJin University Renai College


Regional culture is not a given and relatively fixed thing, but on the contrary, it is self-cultivating. If we want to maintain any type of real culture, it depends on our ability to generate a dynamic form of regional culture. At the same time, it absorbs external influences on both the human level of culture and civilization.

In the "Newborn-Tree Burial Park Design in the Post-Industrial Era" project that I participated in, two parts, the material level and the spiritual experience level, were used to complete the transformation of the regional spirit of the place. At the material level, through the height difference of the site, traditional tomb form specifications are combined with tree burials. People can choose their own funeral method according to their own concepts; at the spiritual experience level, in order to solve the problem of local people worshipping their ancestors, Next to the tomb area, there is also an ancestor worship area and a temple for worship, while the theater area can perform Puxian opera for local residents or puppet shows specially for "gods" and "dead people".


LOCAL FUNERAL CULTURE ANALYSIS



DESIGN STRATEGY

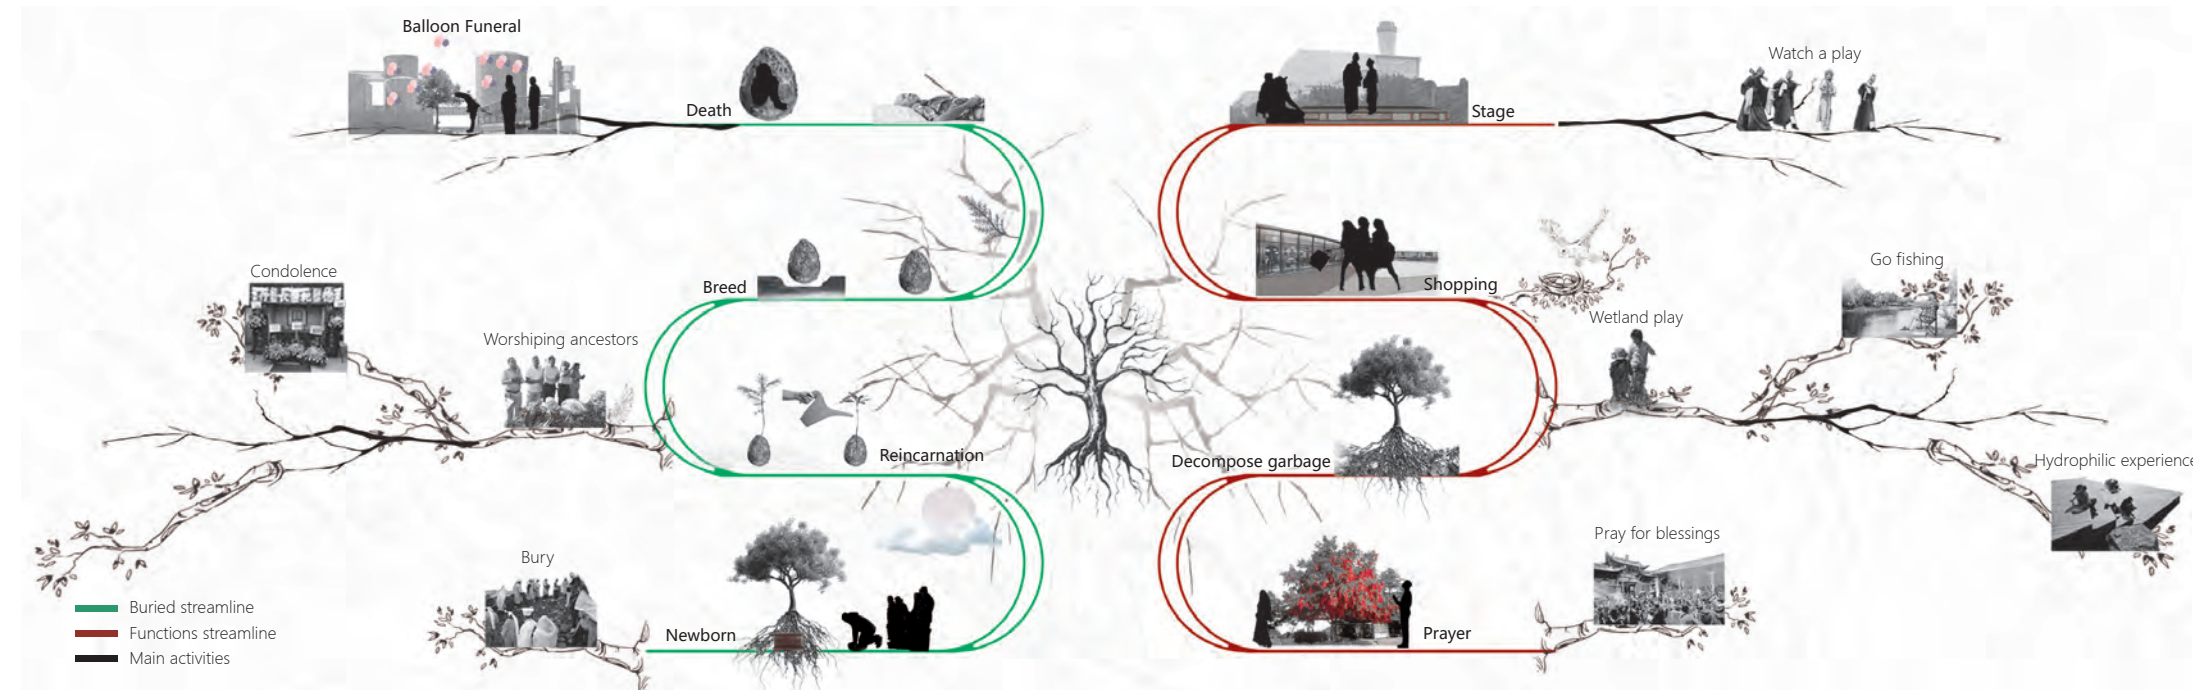


SITE ANALYSIS

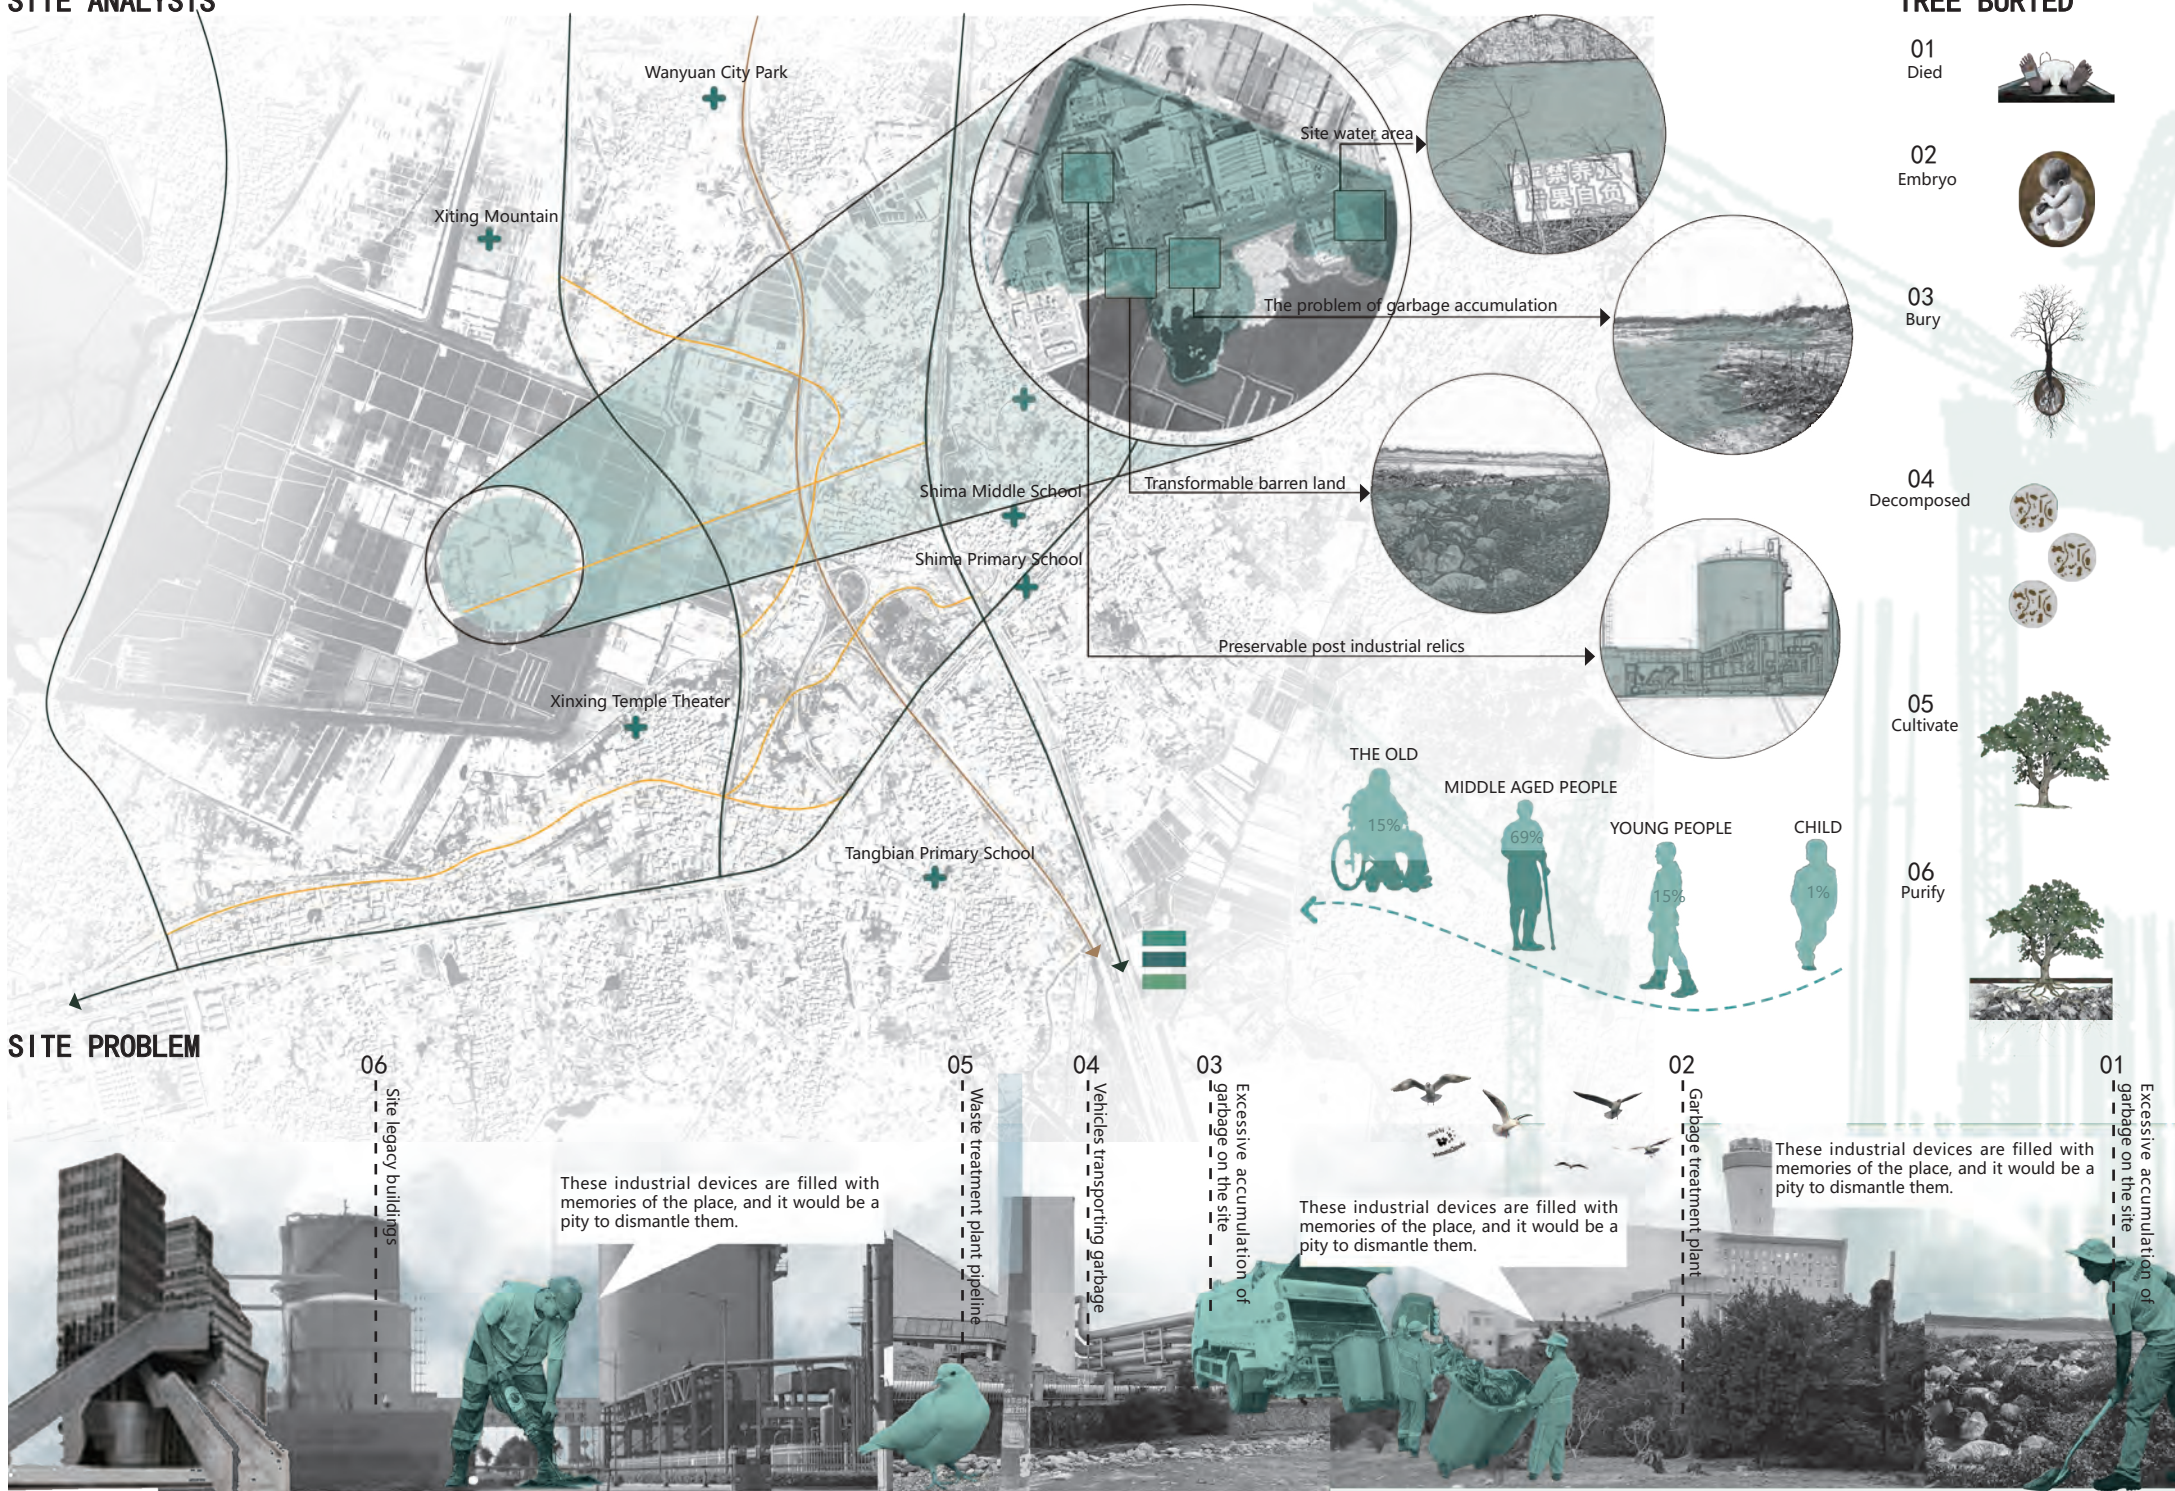


TREE BURIED




FUNCTIONAL DIVISION

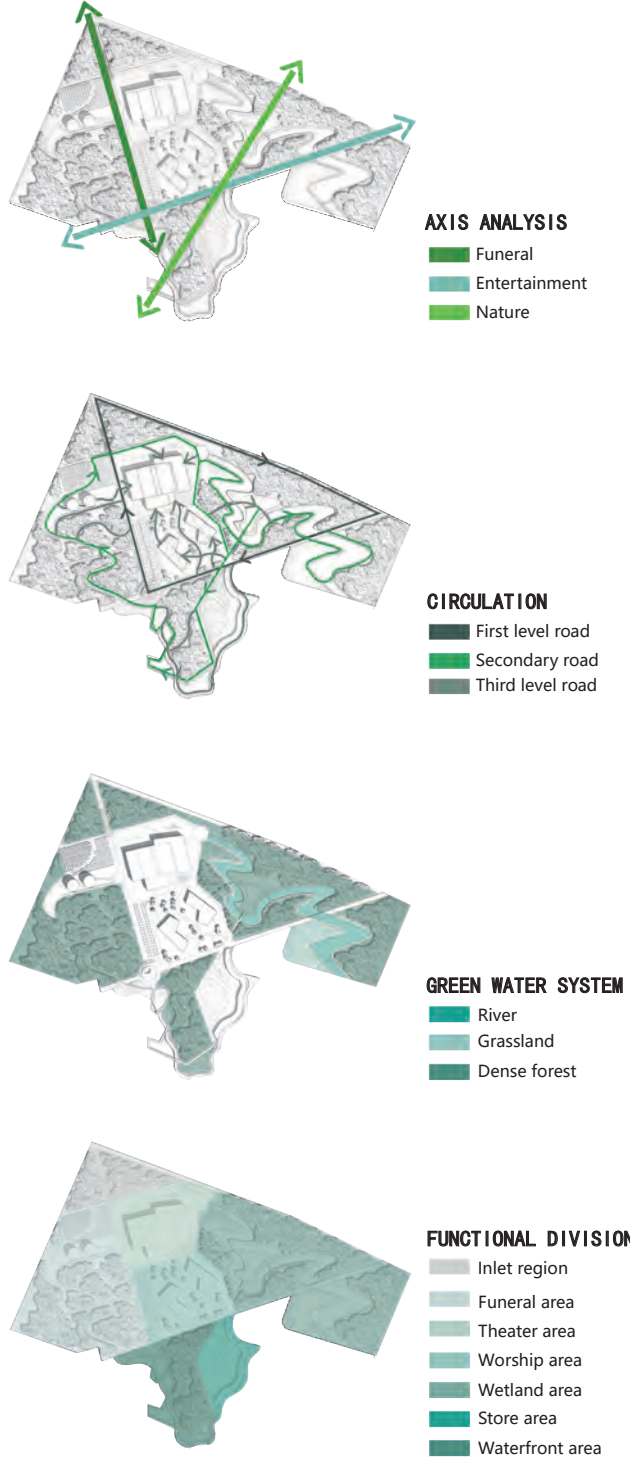


SITE MASTER PLAN

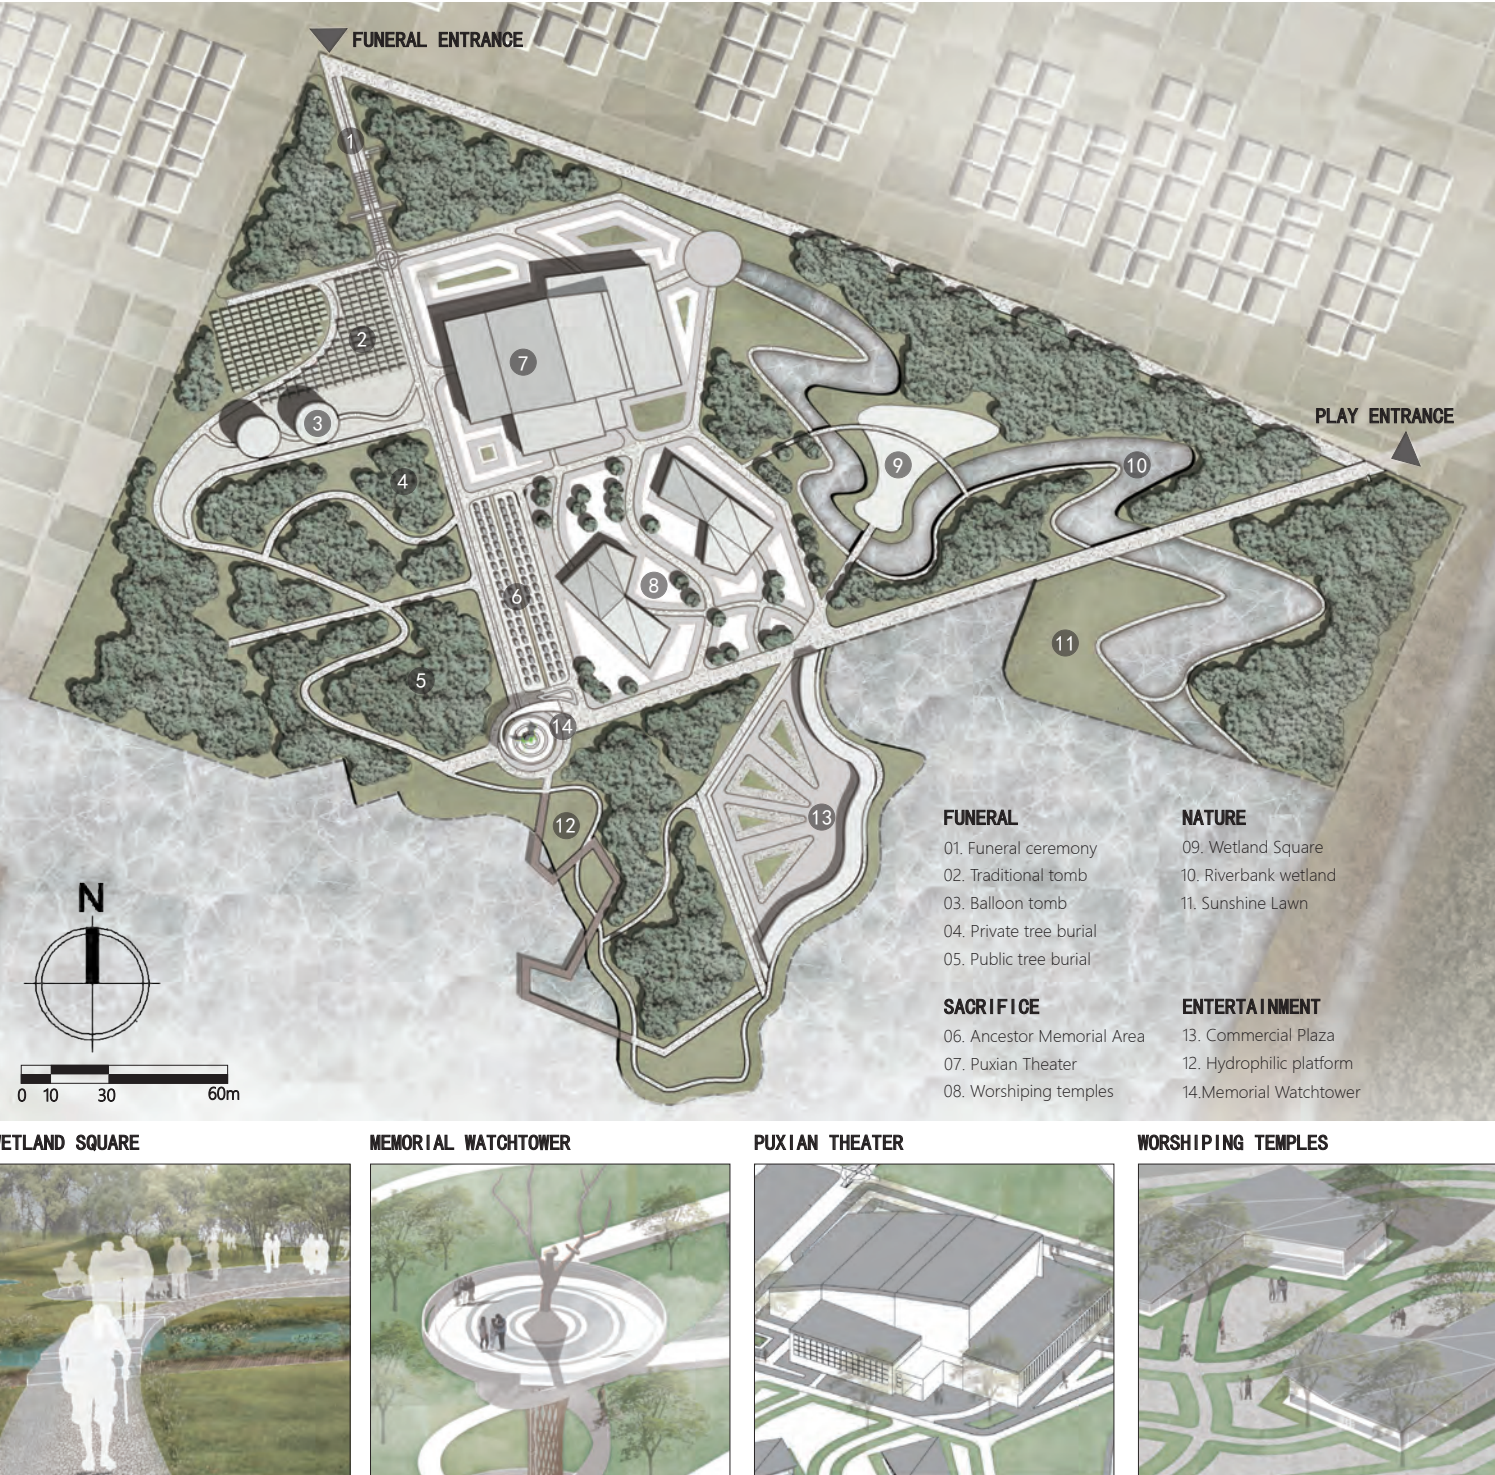

SITE MASTER PLAN

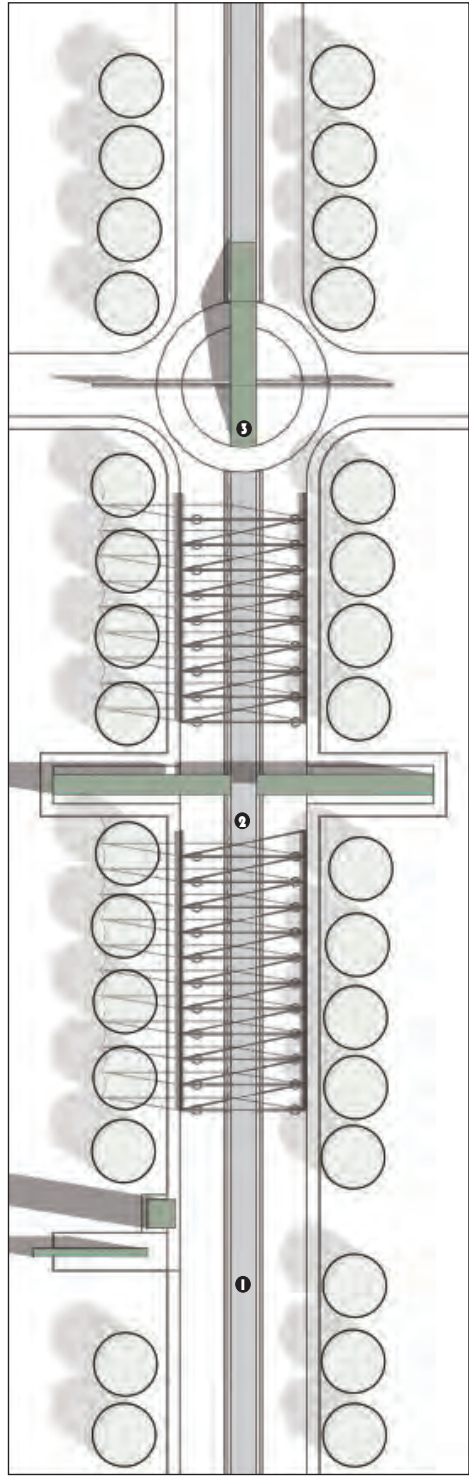

CHINESE TRADITIONAL FUNERAL

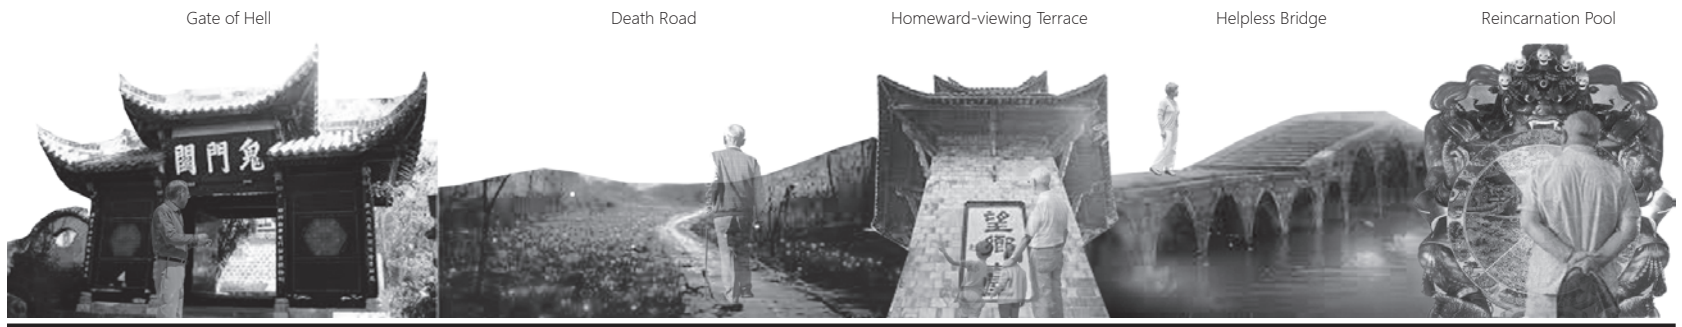

After death, souls pass through the ghostly Gate of Hell, traverse the Death Road, cast Pnal longings from the Homeward-viewing Terrace, drink Meng Po's soup on the Bridge of Helplessness to wash away past memories, and then plunge into the Reincarnation Pool, awaiting rebirth.




■ WANDERING ■ NOSTALGIC ■ FAREWELL ■ RE INCARNATION

ELEVATION




At the entrance of the ceremony, people are engulfed in a haze of bewilderment and incomprehension surrounding death. As they progress along the ritual path, this confusion slowly morphs into a profound sense of loss and yearning for the departed. At the culmination of the ceremony, amid the poignant stillness, they stand around the deceased to bid their Pnal farewell. With heavy hearts and teary eyes, they watch as the departed embarks on a slow journey to the realm of reincarnation, fading away at the threshold between life and death.


WETLAND SQUARE

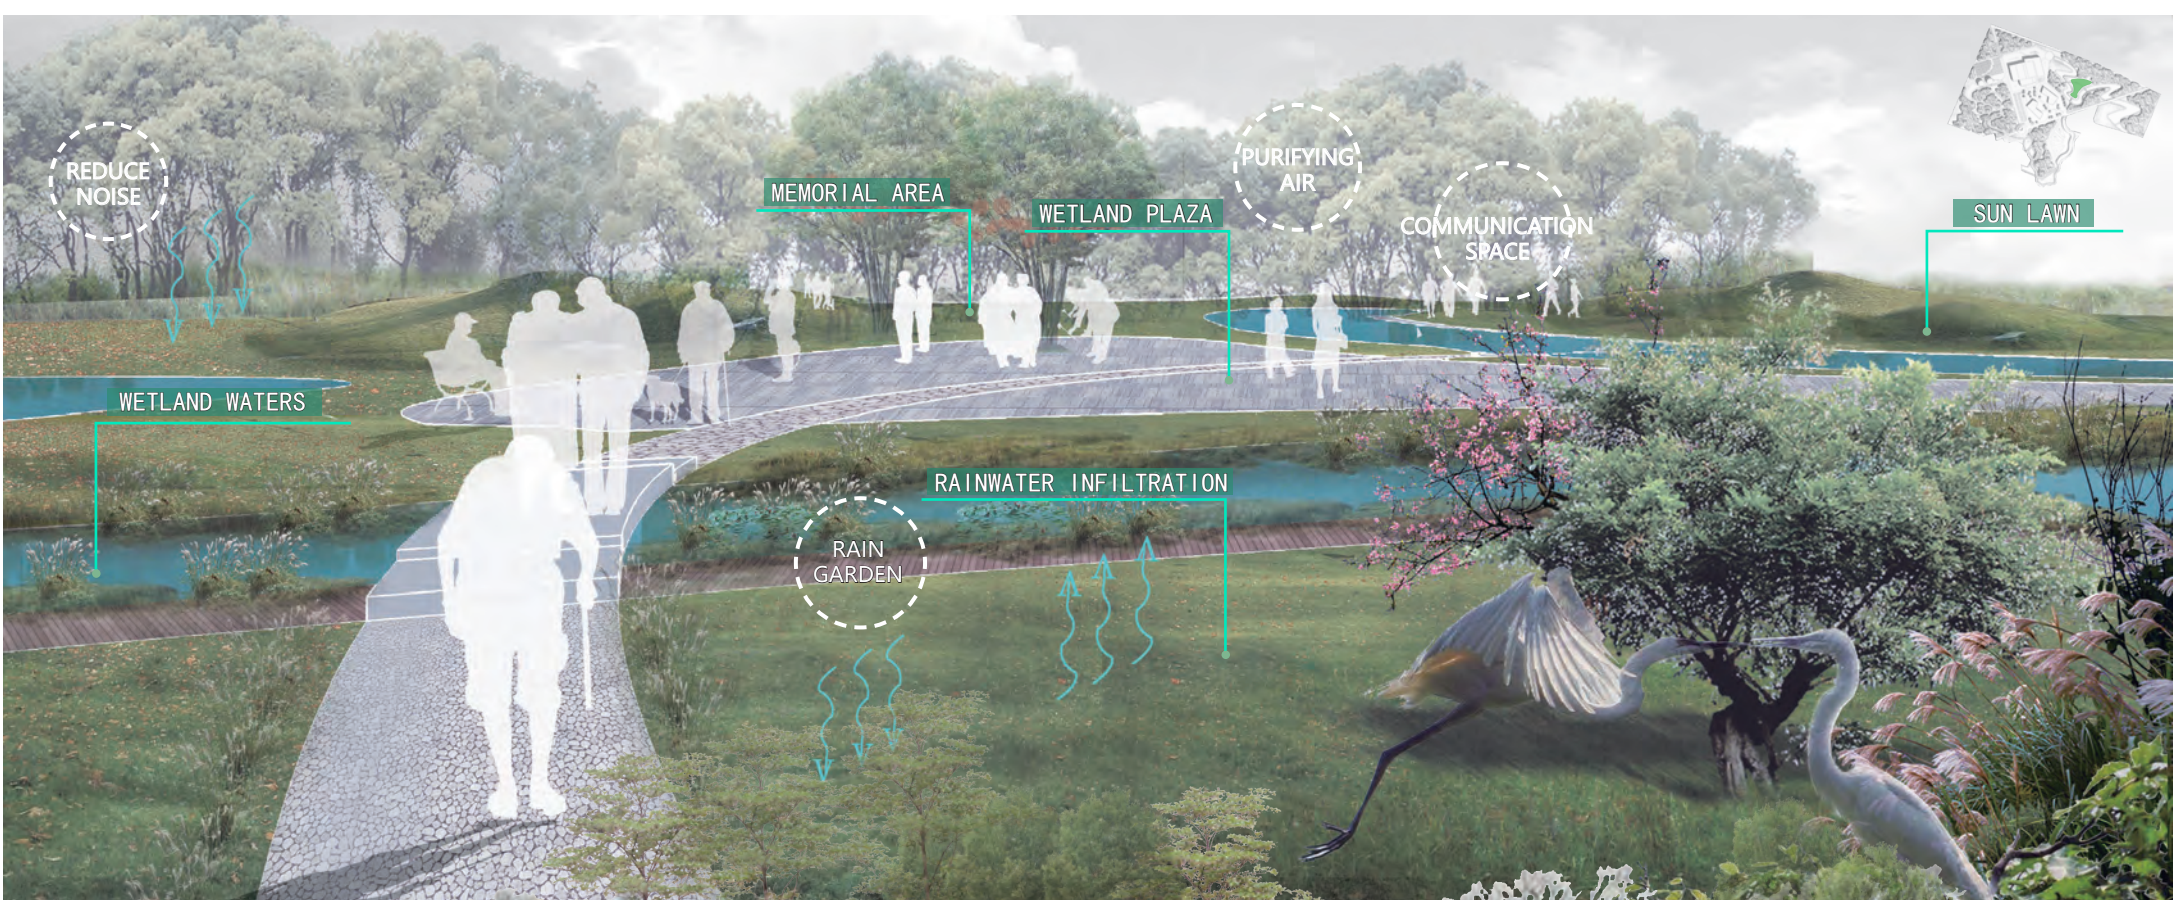


RAINWATER INFILTRATION

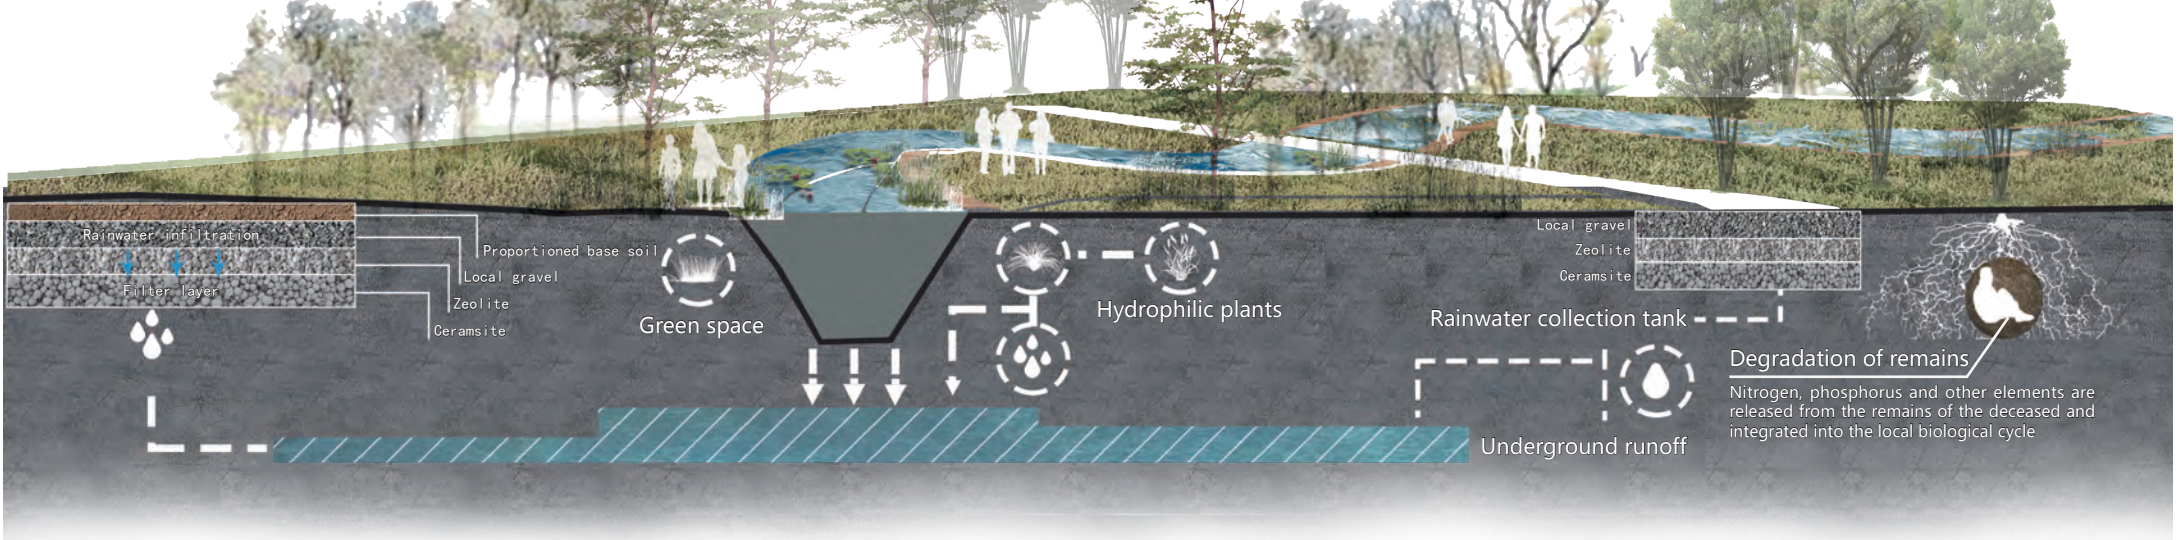


INCONVENIENCES OF LIFE FOR BLIND PEOPLE

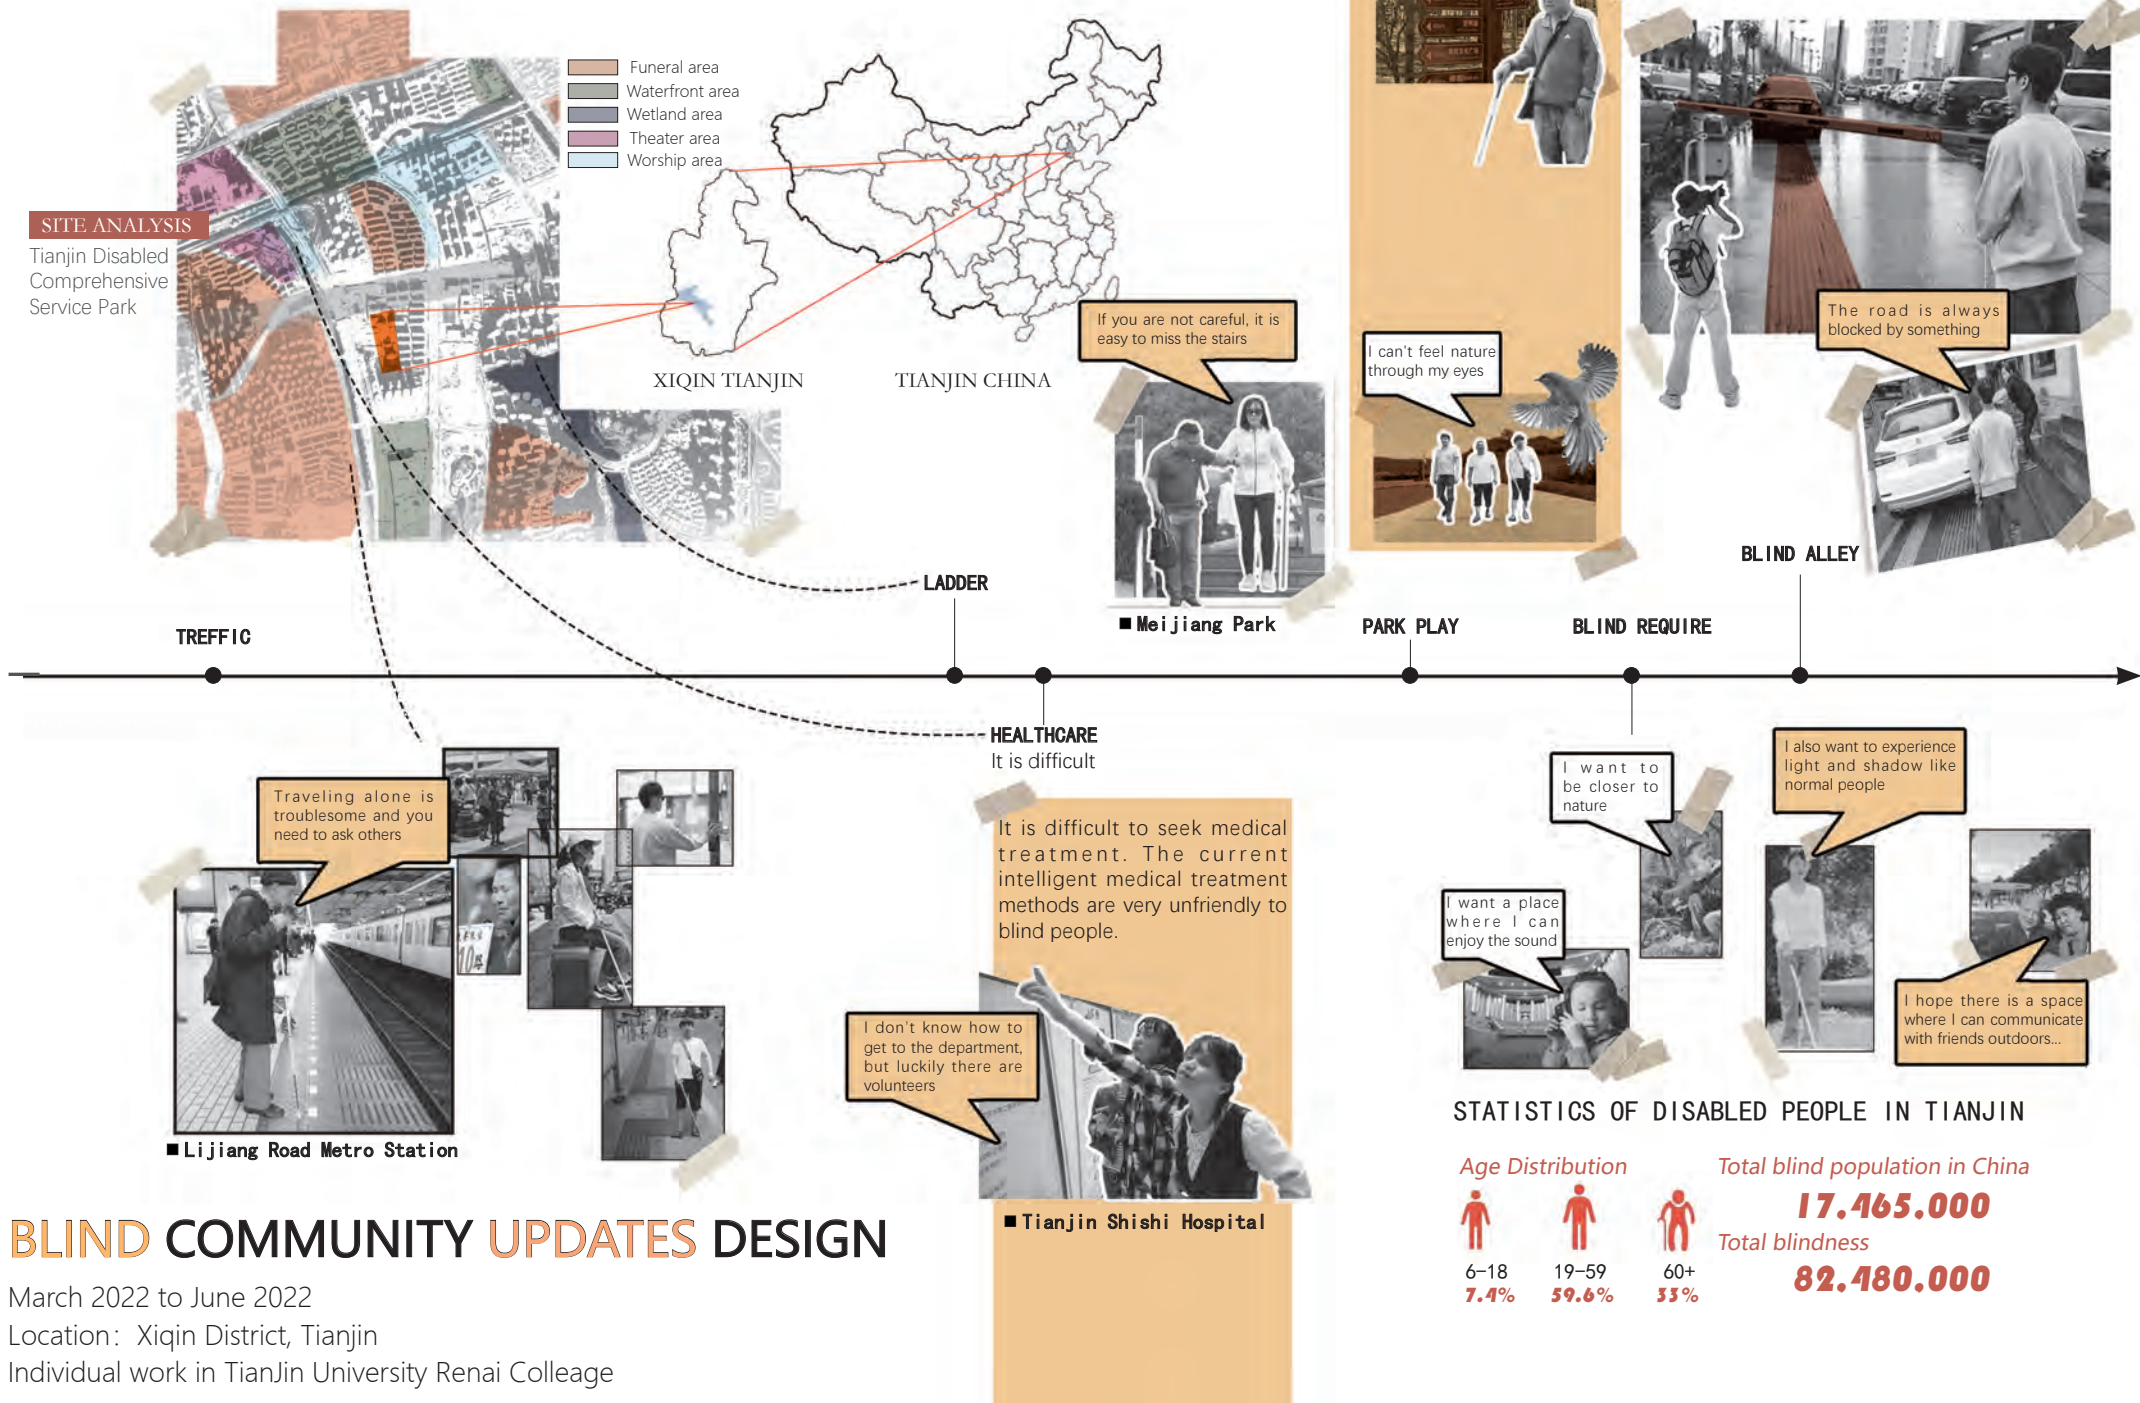


BLIND SENSES

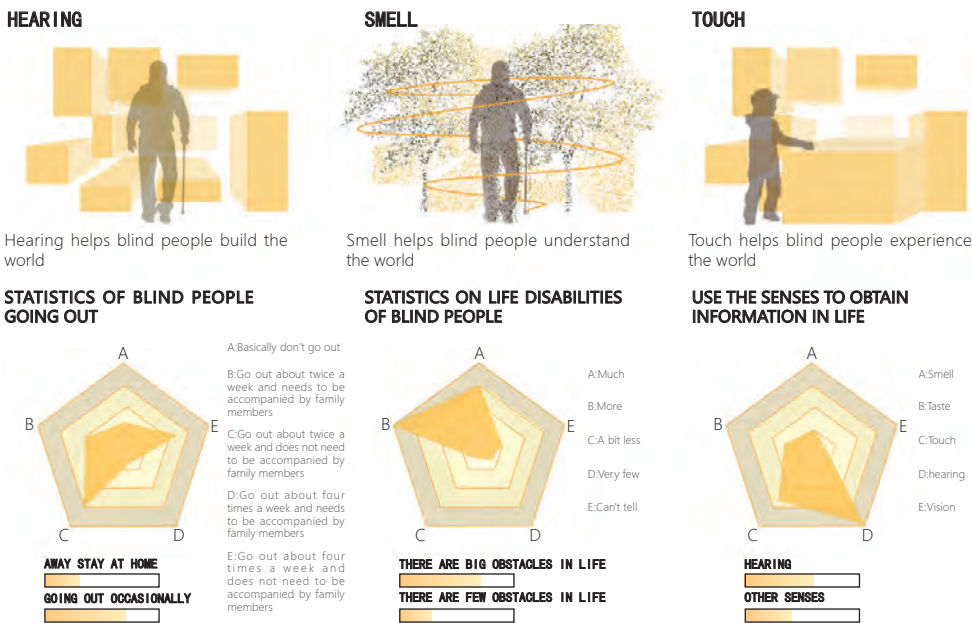


DESIGN STRATEGY

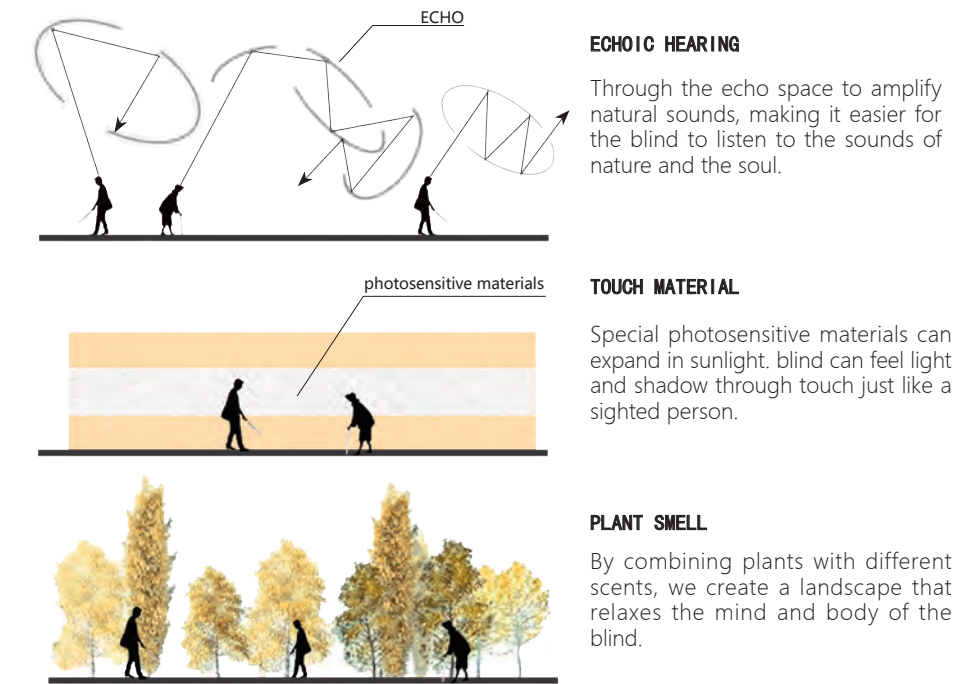


DESIGN STRATEGY

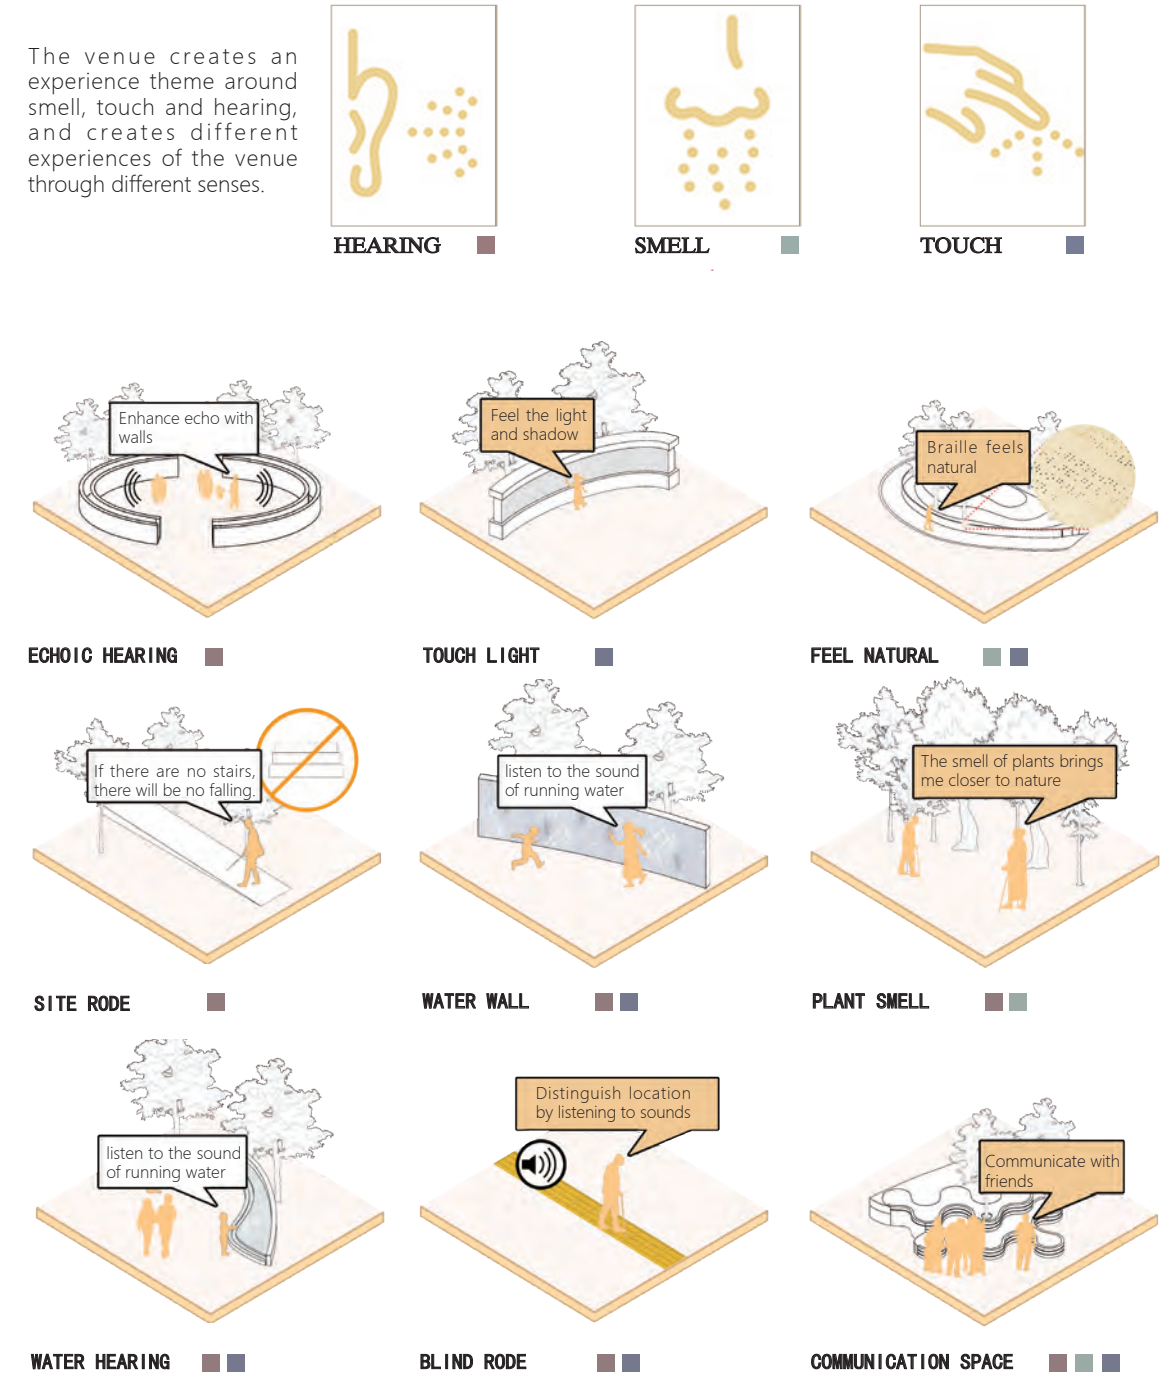


SITE MASTER PLAN

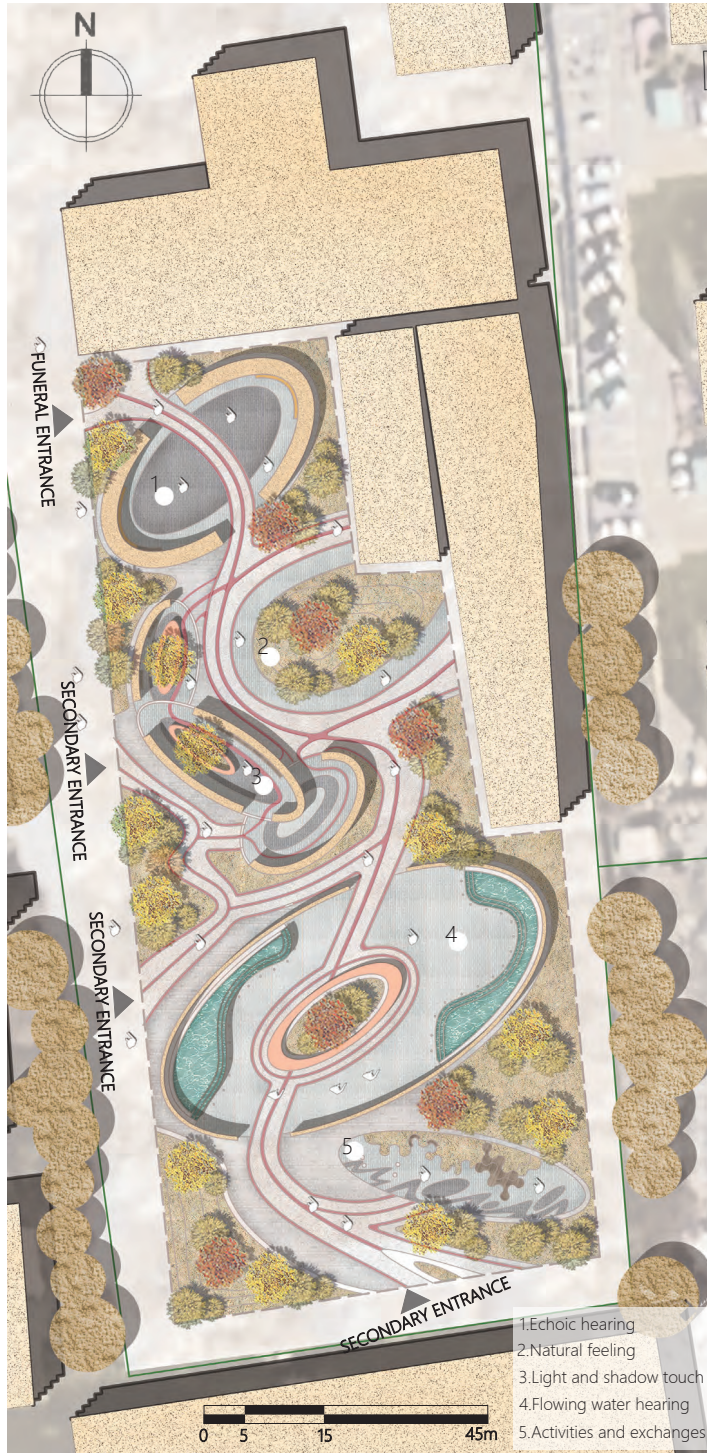



FUNCTIONAL DIVISION

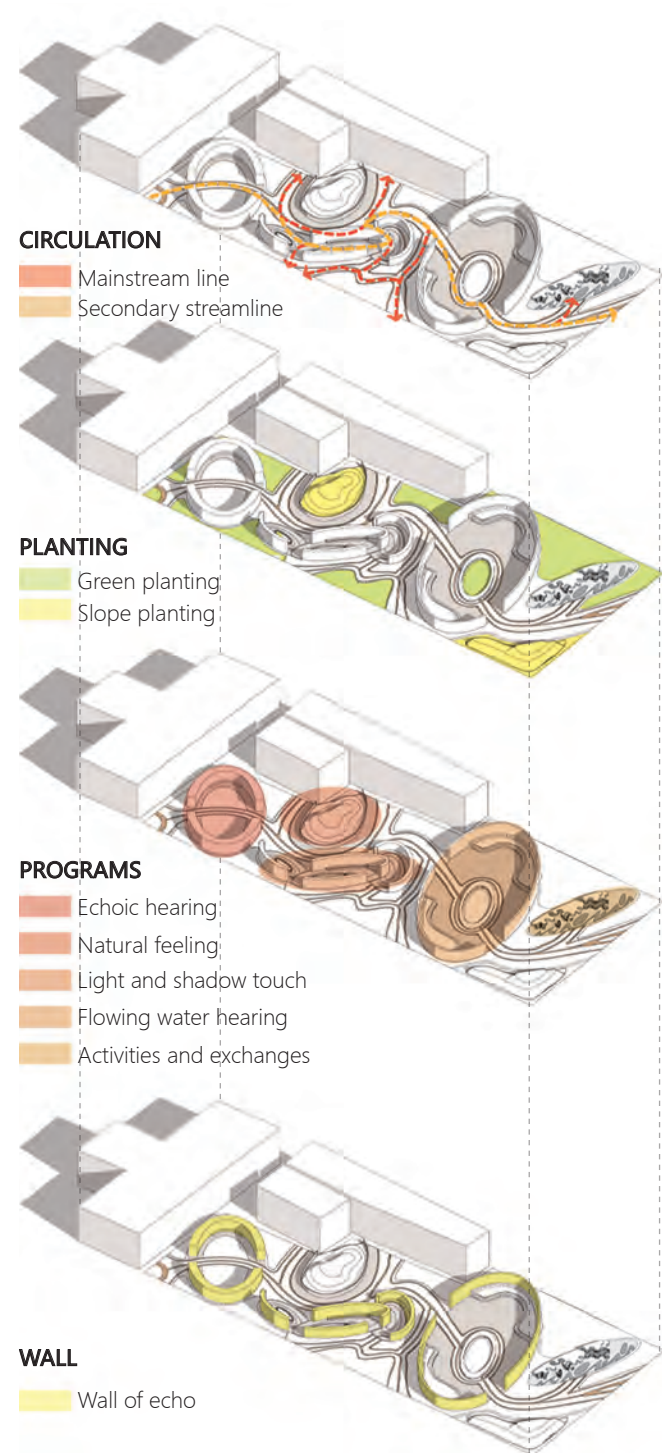

SITE PLANT

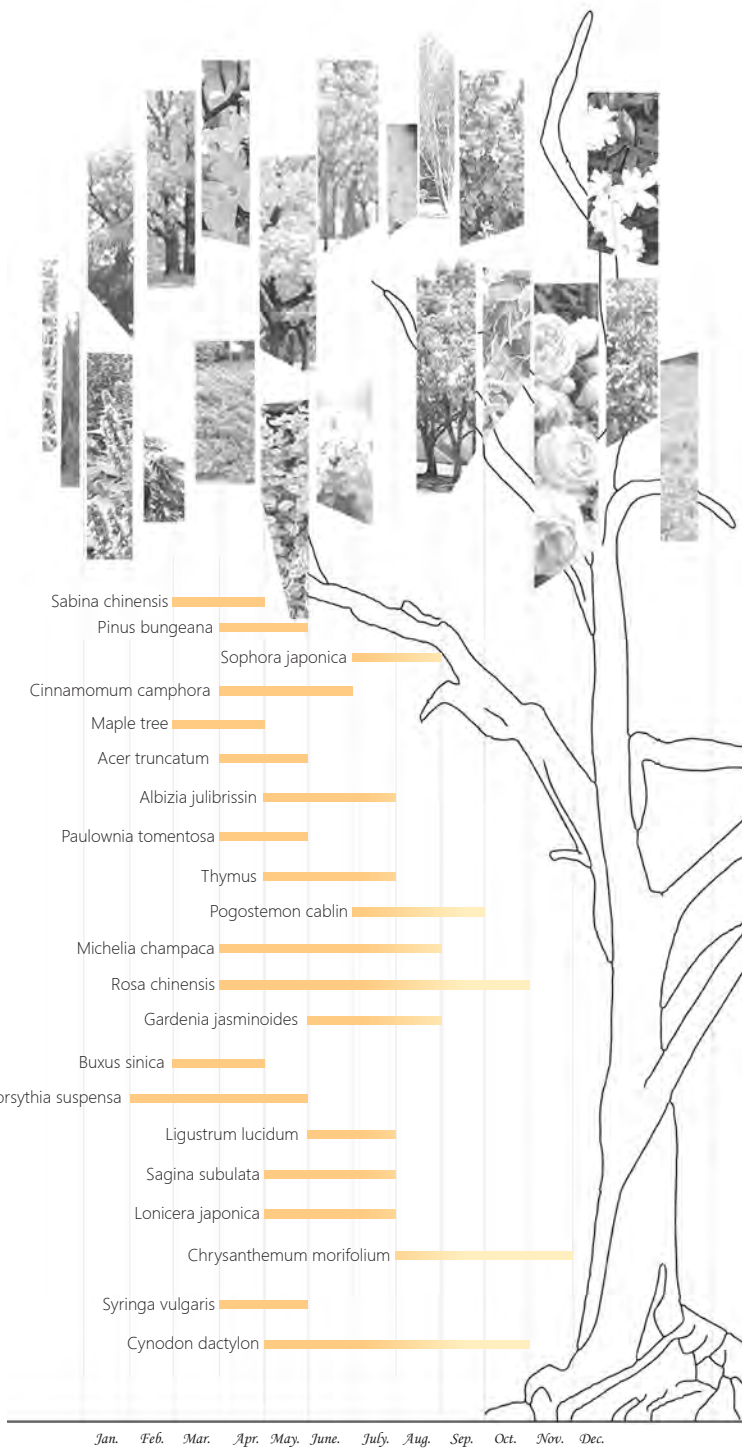

AREA 3 DESIGN — LIGHT AND SHADOW TOUCH

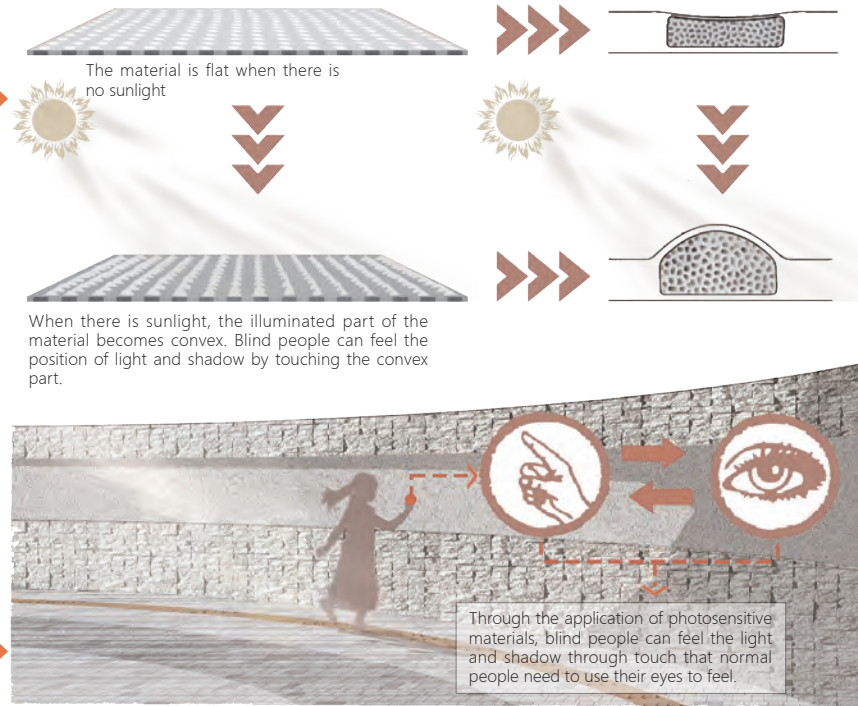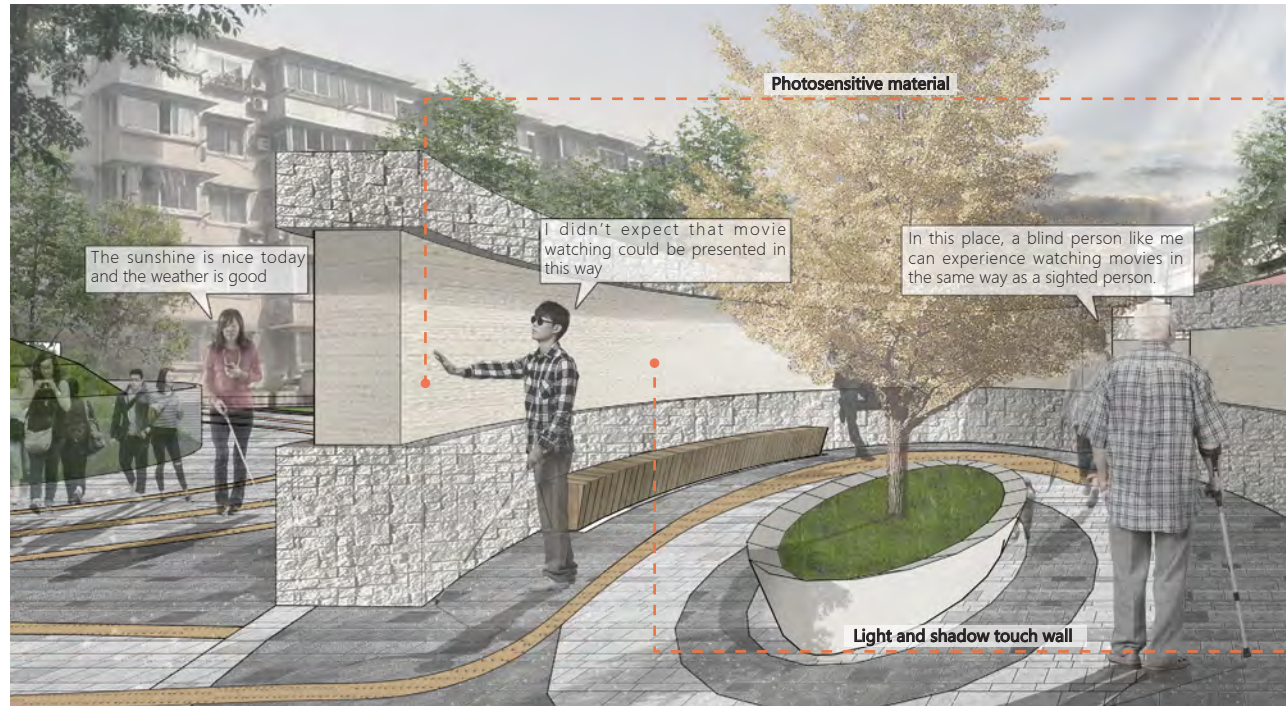

AREA 4 DESIGN — FLOWING WATER HEARING

